



LEGEND

- | | |
|---------|--|
| — — — — | MAIN GROUND GRID #2/0
INSULATED GREEN, COPPER |
| ● | GROUND CONNECTION TO PILES/
EQUIPMENT |
| — ■ — — | GROUND TAP WITH TEE CONNECTION |

NOTES:

1. MODULE PILES TO BE USED AS GROUNDING RODS.
2. ALL TAPS SHALL BE #2 SUITABLE FOR CONDUCTOR SIZE AND TYPE.
3. ALL TAPS SHALL BE COATED WITH GYPLANT AND SHALL BE TAPED WHERE REQUIRED.
4. GROUND GRID TO BE TIED TO SITE GROUNDING BY FIELD ELECTRICAL CONTRACTOR.
5. MODULE ELECTRICAL CONTRACTOR TO BOND TRAY GROUND TO MODULE AT OPPOSITE CORNERS OF MODULE AND PROVIDE 3 METER PIGTAIL COILED AND TAPED TO SIDE OF SKID FOR CONNECTION TO PILES BY FIELD ELECTRICAL CONTRACTOR.
6. MODULE CONTRACTOR TO FABRICATE CABLE TRAY SUPPORT.
7. MODULE CONTRACTOR TO INSTALL A #2 AWG GREEN W/ YELLOW STRIPES GROUND WIRE FROM RIO PANEL TO MODULE STRUCTURAL STEEL.
8. FOR DETAILS, REFER TO ELECTRICAL STANDARD INSTALLATION DRAWINGS.
9. ALL CABLES SHALL BE PROTECTED BY 1/2" AIN STEEL GROUNDING GROUP. SHALL BE COVERED UP TO 2 METERS ABOVE THE FLOOR/ GROUND LEVEL.
10. THIS STEEL SUPPORT IS RESERVED FOR SITE SPECIFIC ENGINEERING TO MOUNT MV-JUNCTION BOX AND FIBER OPTIC JUNCTION BOX. THIS POST SHALL NOT BE USED FOR ANY OTHER PURPOSES.
11. WARNING LAMICOID SHALL BE AFFIXED TO MV CABLE TRAY EVERY 10m along the CABLE TRAY (SEE DETAIL ABOVE RIGHT).
12. UTILITY RECEPTACLE FED BY HTP-101 FROM INJECTION MODULE BY FIELD CONTRACTOR.
13. 450mm CABLE TRAY TO BE SHIP LOOSE AND FIELD FIT TO BRIDGE THE GAP BETWEEN THE 450mm VERTICAL 90° FITTING ON INJECTION MODULE TO THE 300mm CABLE TRAY ON PROJECTION MODULE WITH THE REDUCER PLATE, INSTALLED BY FIELD CONTRACTOR.
14. JUNCTION BOX JBHT-P01 TO BE INSTALLED WITH DOOR SWING LEFT TO RIGHT. DETAIL DIAGRAM SHOWN ON G02-1-PRDXXX-E-JB-01-P01-01.

SHOP NOTES:

1. ALL ITEMS ON THIS MODULE (EXCLUDING MANUAL VALVES) INCLUDE THE TAG PREFIX PRD0154.

ENGINEERING NOTES:

1. THIS DRAWING REFERENCES THE ENGINEERING RECORD G02-1-PRDXXX-E-GA-01-P01-01 REV 0 FOR ALL TECHNICAL INFORMATION. IN THE EVENT OF DISCREPANCY BETWEEN THIS DRAWING AND THE ENGINEERED DRAWING OF RECORD, THE ENGINEERED DRAWING OF RECORD WILL TAKE PRECEDENCE UNLESS THE CHANGE IS PROPERLY CLOUDED AS A REVISION TO THIS DRAWING AND STAMPED BY A PROFESSIONAL ENGINEER.

LAMICOID DETAIL



(WHITE LETTERS ON RED BACKGROUND)

DANGER - HIGH VOLTAGE

LAMICOID SHALL BE 125mm X 550mm
SHALL BE OF ADHESIVE TYPE
(NO HOLES FOR MOUNTING)

ELECTRICAL BILL OF MATERIALS

ITEM NO.	QTY.	DESCRIPTION	MANUFACTURER	CATALOG/PART NO.	SUPPLIED BY	REMARKS
1	1	REMOTE I/O PANEL, RIO-P01	SPARTAN CONTROLS	TBD	SCOVAN ENG.	INSTALLED BY SCOVAN SHOP
2	1	HEAT TRACE JUNCTION BOX NEMA4, JBHT-P01	HOFFMAN	CSD242412	SCOVAN SHOP	INSTALLED BY SCOVAN SHOP
3	1	SAFESITE LINEAR, 3850 LUMENS (2FT), 29 WATTS, 100-277 VAC, COOL WHITE 5000K, CLEAR POLYCARBONATE LENS, LOW PROFILE c/w MOUNTING BRACKET, ZONE 2	DIALIGHT	LPD3C4D2P c/w LPXW4	SCOVAN SHOP	INSTALLED BY SCOVAN SHOP
4	1	20A, 120V RECEPTACLE ASSEMBLY C/W GROUND FAULT PROTECTION AND TWO GANG BOX, ZONE 1 & 2 APPROVED. DEAD END OR FEED THROUGH AS REQUIRED	COOPER CROUSE HINDS	CPS152R & GFS-1 C/W EDS BOX AS REQ'D	SCOVAN SHOP	INSTALLED BY SCOVAN SHOP
5	A/R	ALUMINUM CABLE TRAY, CLASS E LOAD RATING, 300mm WIDE, 152 mm SIDE RAILS, 6 m LONG, LADDER STYLE, 225mm RUNG SPACING	UNITRAY	SLA-86054	SCOVAN SHOP	INSTALLED BY SCOVAN SHOP
6	A/R	ALUMINUM CABLE TRAY, CLASS E LOAD RATING, 450mm WIDE, 152 mm SIDE RAILS, 6 m LONG, LADDER STYLE, 225mm RUNG SPACING	UNITRAY	SLA-86064	SCOVAN SHOP	INSTALLED BY SCOVAN SHOP
7	1	ALUMINUM CABLE TRAY, CLASS E 90° VERTICAL OUTSIDE ELBOW, 300mm WIDE, 300mm RADIUS, 152 mm SIDE RAILS, LADDER STYLE	UNITRAY	90A-8354	SCOVAN SHOP	INSTALLED BY SCOVAN SHOP
8	A/R	CABLE TRAY BARRIER STRIP, ALUMINUM, 3m STRAIGHT SECTION, c/w SCREWS	UNITRAY	SBA-4	SCOVAN SHOP	INSTALLED BY SCOVAN SHOP
9	1	CABLE TRAY BARRIER STRIP, ALUMINUM, 90° VERT. OUTSIDE ELBOW, c/w SCREWS	UNITRAY	OBA-493	SCOVAN SHOP	INSTALLED BY SCOVAN SHOP
10	A/R	ALUMINUM TRAY COVER, SOLID WITH FLANGE, 300mm WIDE	UNITRAY	SLA-8305S	SCOVAN SHOP	INSTALLED BY SCOVAN SHOP
11	A/R	ALUMINUM TRAY COVER, SOLID WITH FLANGE, 450mm WIDE	UNITRAY	SLA-8306S	SCOVAN SHOP	INSTALLED BY SCOVAN SHOP
12	A/R	ALUMINUM CHANNEL TRAY STRAIGHT 4 INCH (100mm)	THOMAS & BETTS	ALTC04V3	SCOVAN SHOP	INSTALLED BY SCOVAN SHOP
13	A/R	ALUMINUM CHANNEL TRAY STRAIGHT 6 INCH (150MM)	THOMAS & BETTS	ALTC06V3	SCOVAN SHOP	INSTALLED BY SCOVAN SHOP
14	A/R	GROUND WIRE, #2/0 TW GREEN	OPEN		SCOVAN SHOP	INSTALLED BY SCOVAN SHOP
15	A/R	GROUND WIRE, #2 TW GREEN	OPEN		SCOVAN SHOP	INSTALLED BY SCOVAN SHOP
16	A/R	COMPRESSION CONNECTOR, #2/0 - #2 AWG	THOMAS & BETTS	CTP202	SCOVAN SHOP	INSTALLED BY SCOVAN SHOP
17	A/R	SERVIT POST CONNECTOR, #2/0 AWG	BURNDY OR EQUAL	K2C26	SCOVAN SHOP	INSTALLED BY SCOVAN SHOP
18	A/R	GROUND CONNECTOR, #4 - #2/0 AWG	BURNDY OR EQUAL	GB26	SCOVAN SHOP	INSTALLED BY SCOVAN SHOP
19	A/R	CABLE TRAY BONDING JUMPER	OPEN		SCOVAN SHOP	INSTALLED BY SCOVAN SHOP
20	A/R	RIGID ALUMINUM CONDUIT, 3/4" DIA.	OPEN		SCOVAN SHOP	INSTALLED BY SCOVAN SHOP

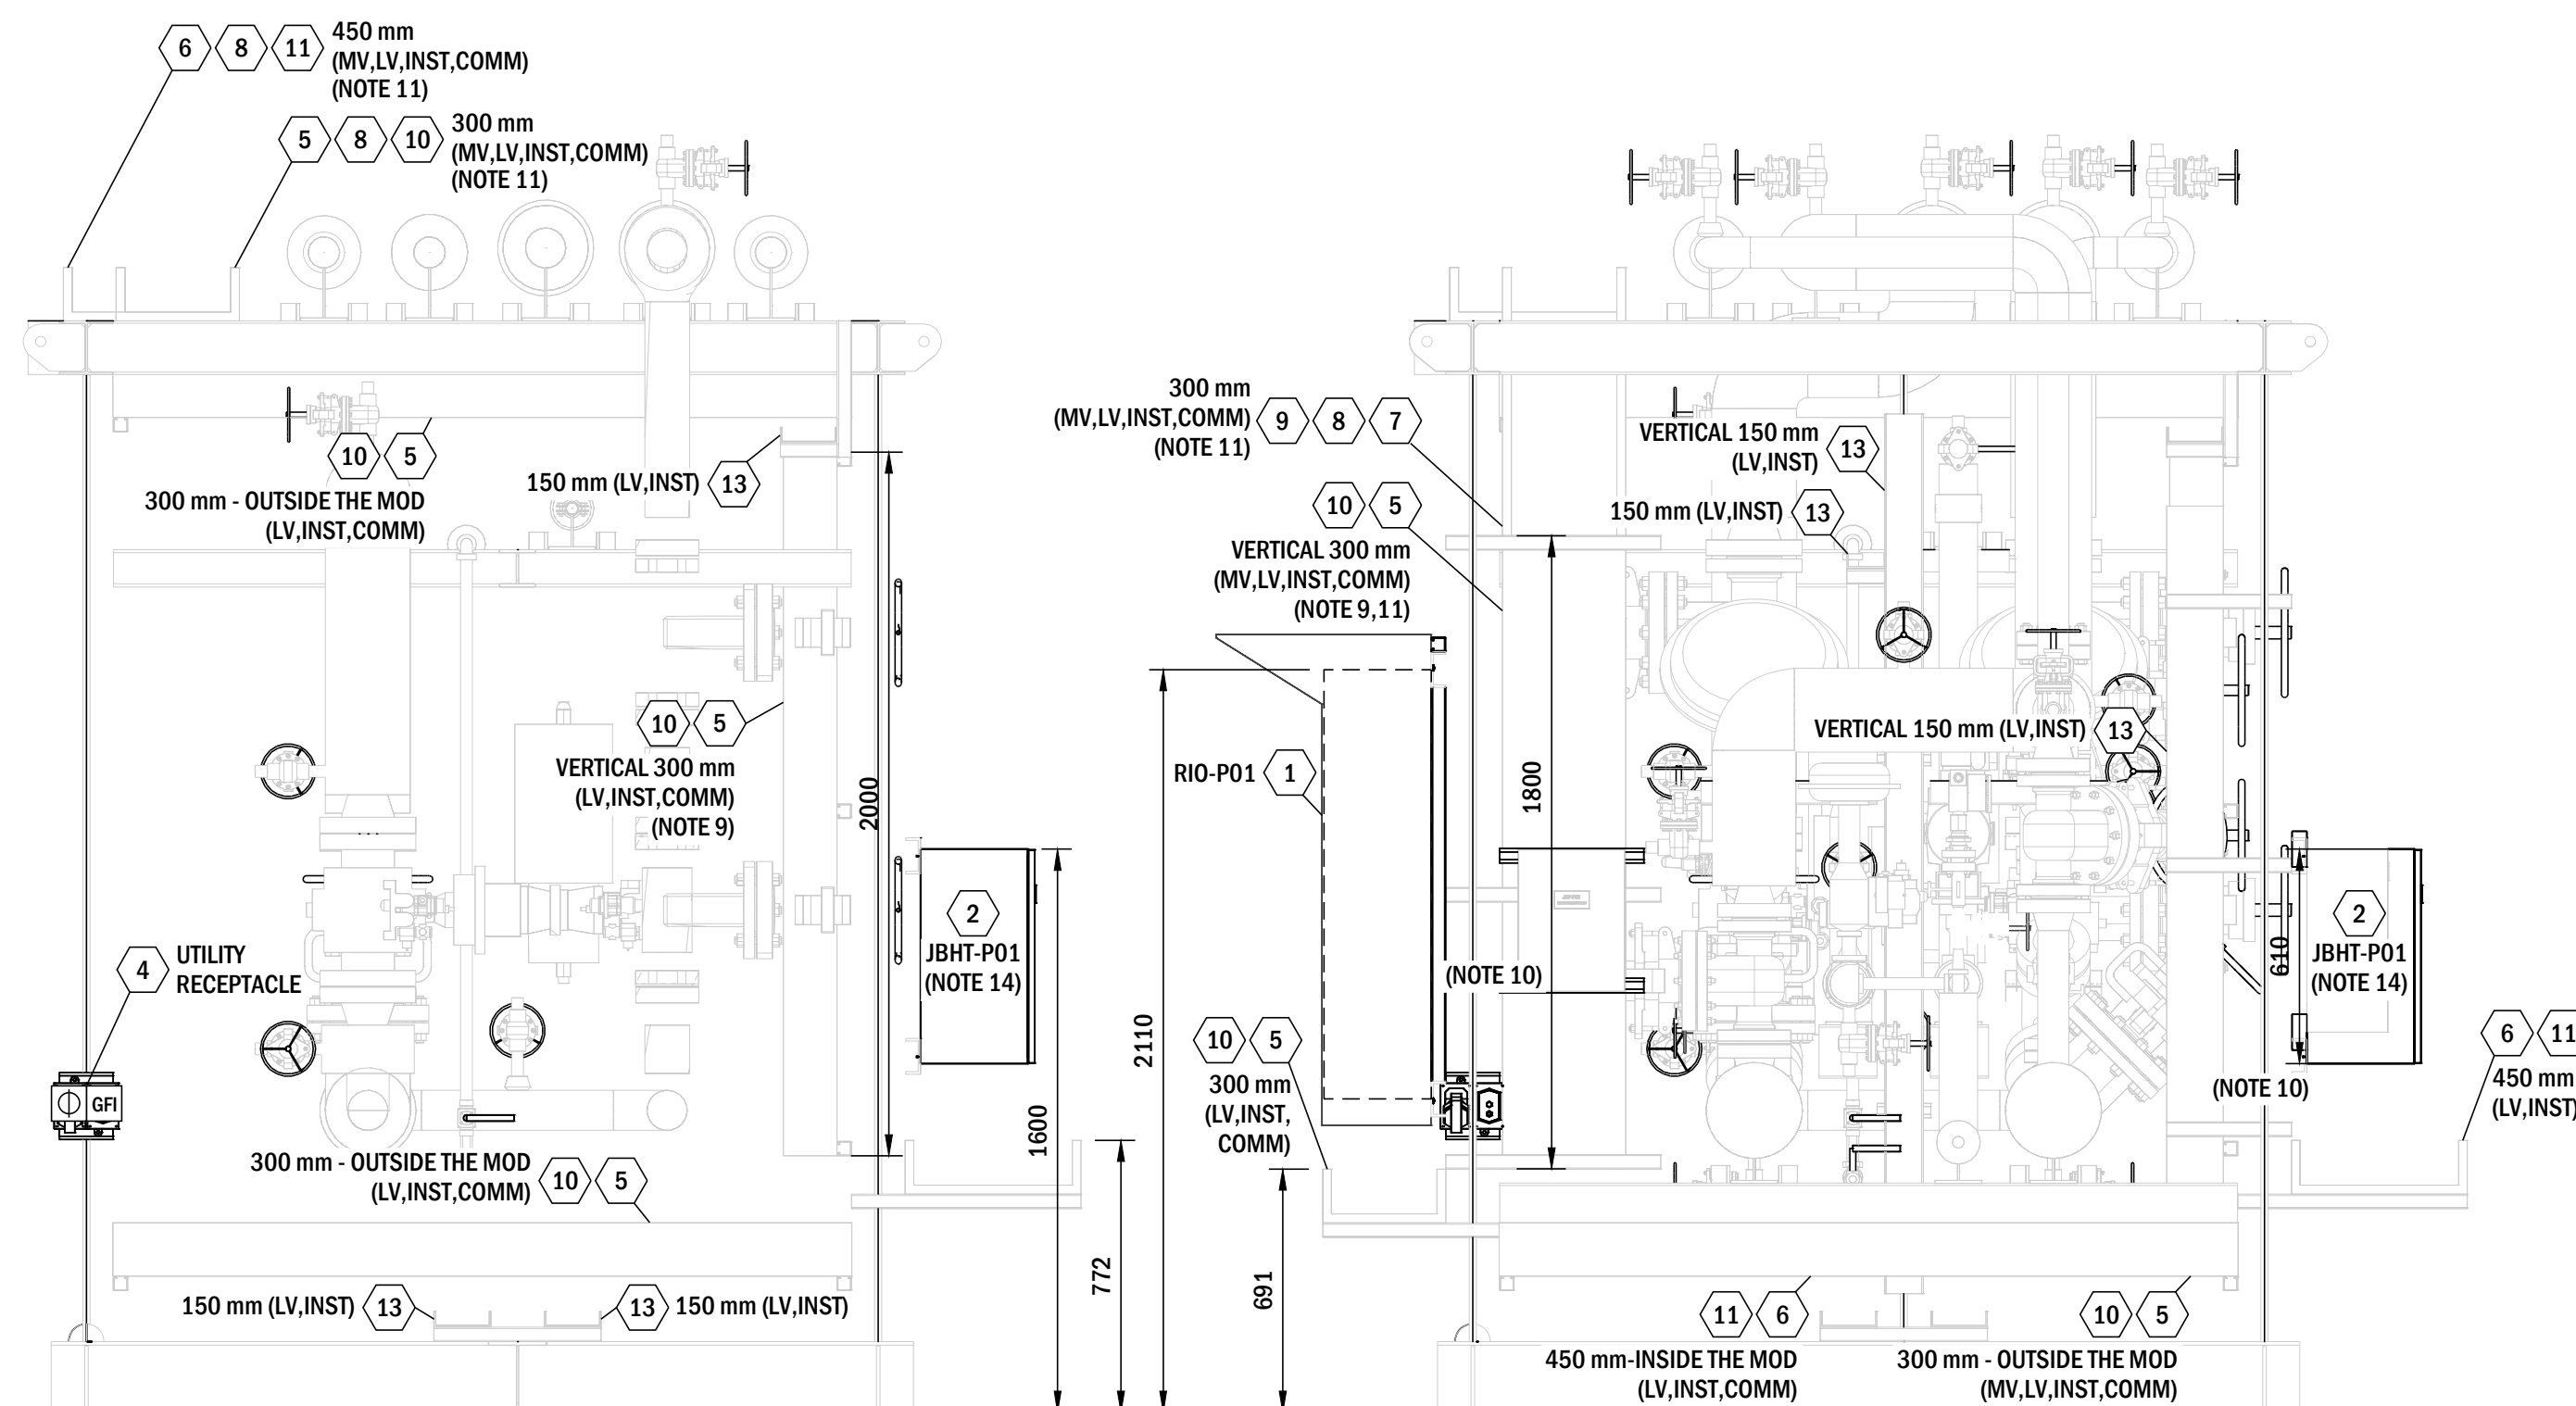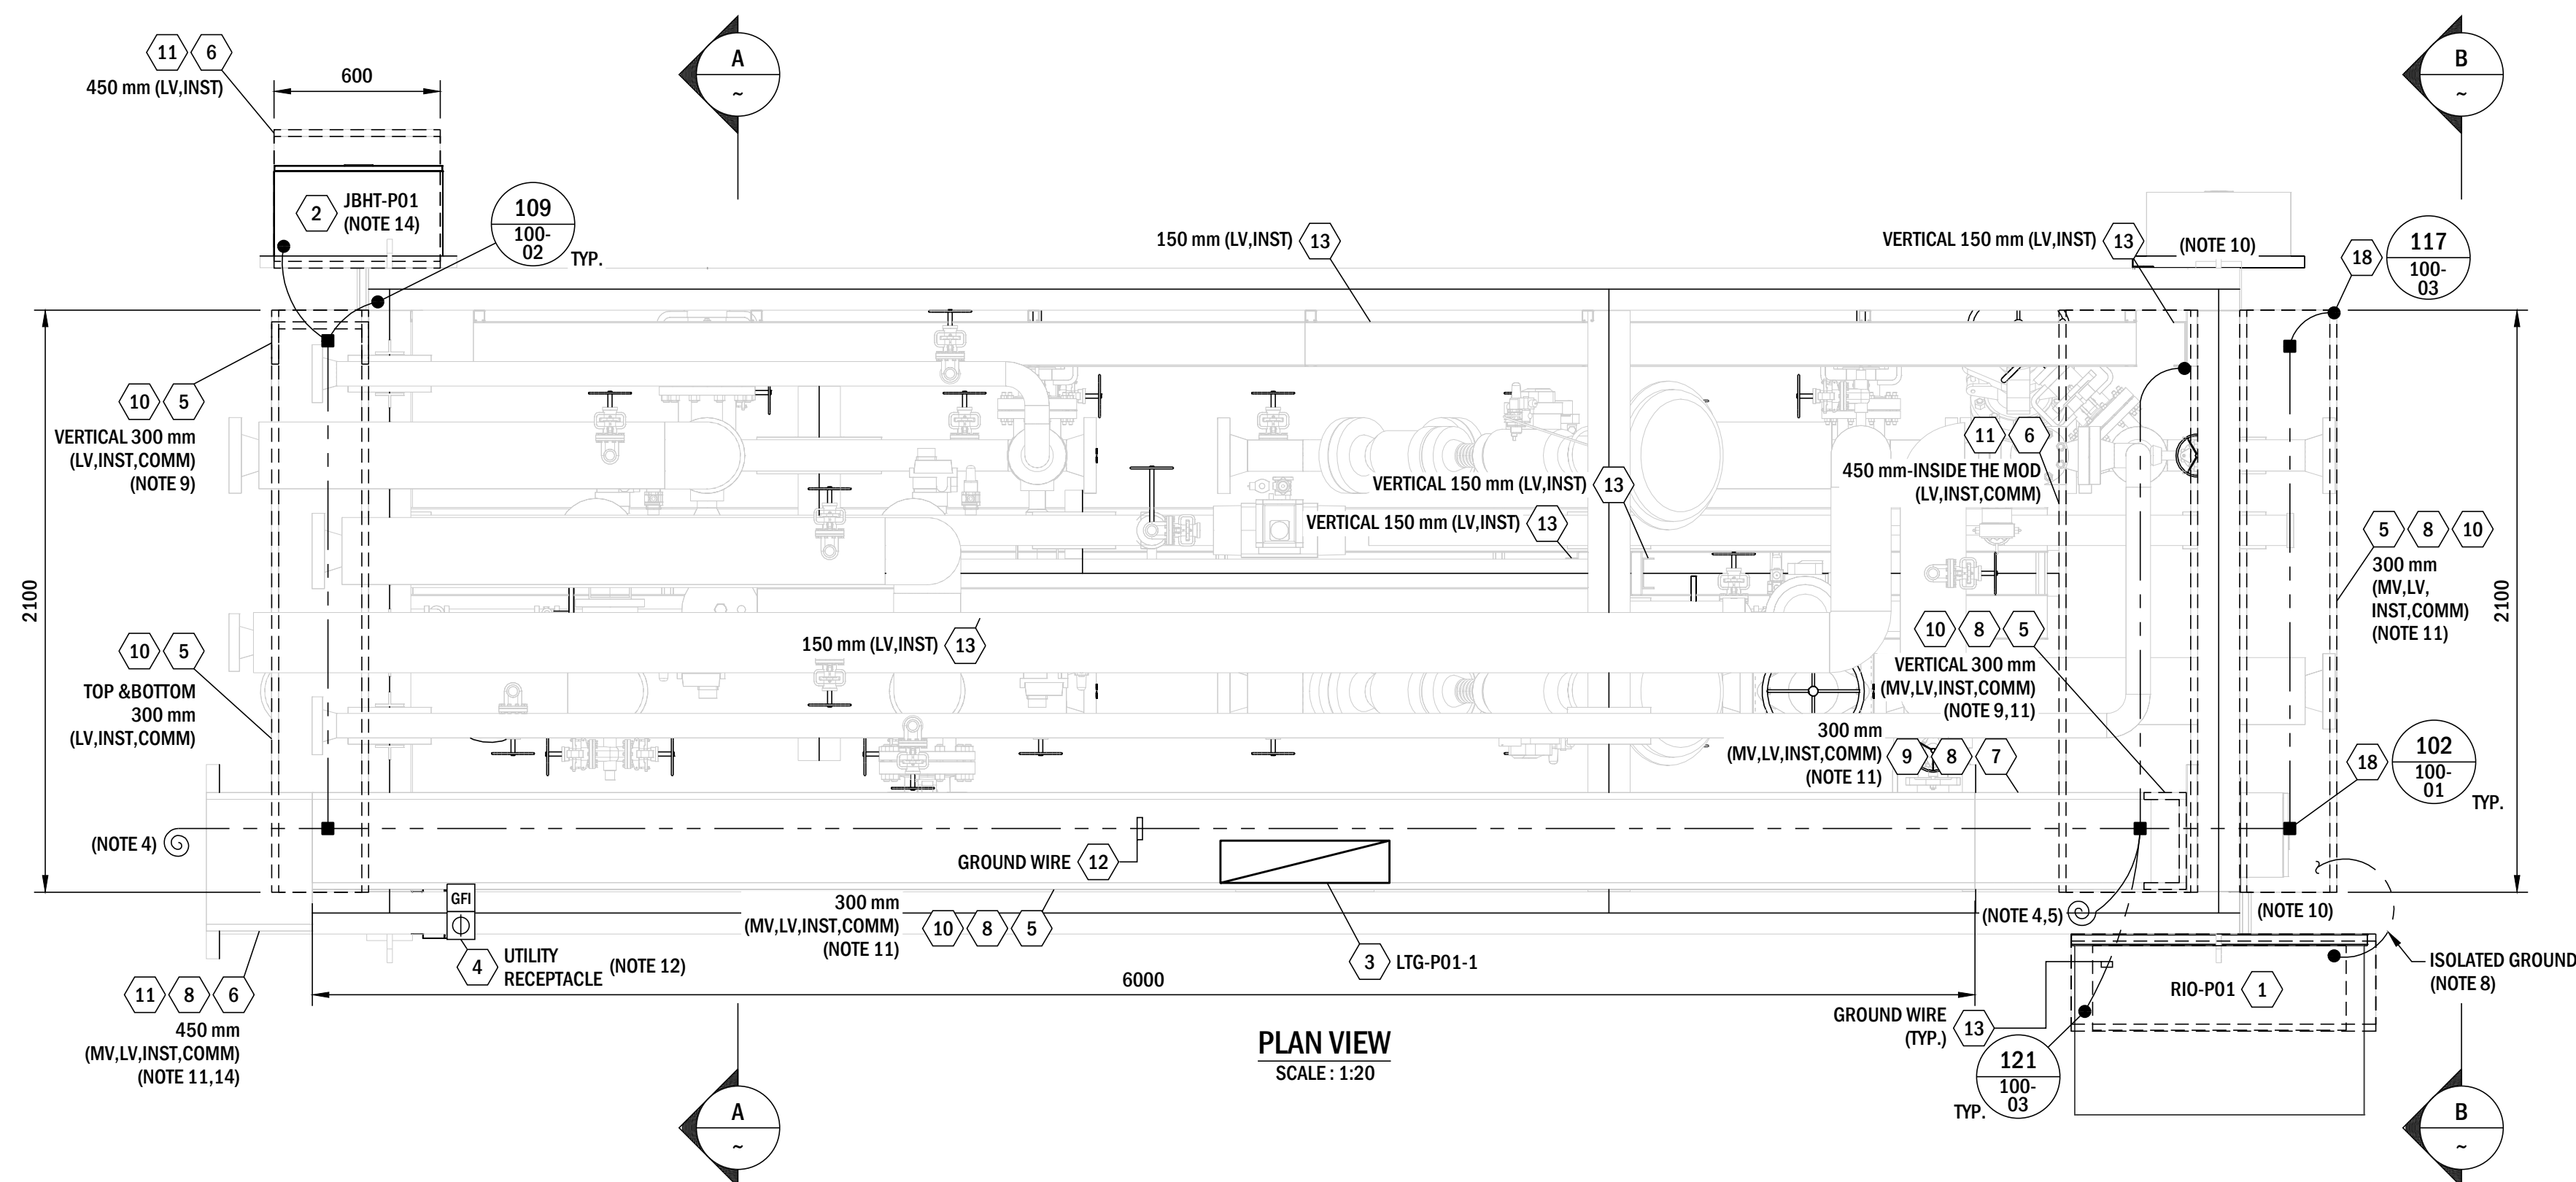


A SECTION VIEW
~
SCALE 1:20

B SECTION VIEW
~ SCALE 1:20

BASE
OPTION 3
OPTION 9

THIS MODULE IS TO BE LOCATED IN A ZONE 2 AREA,
GAS GROUP IIA AND SHALL BE WIRED ACCORDINGLY.
TEMPERATURE CODE IS T2D.
EQUIVALENT PROTECTION LEVELS Ga, Gb, Gc.
(FOR ELECTRICAL PURPOSES ONLY)

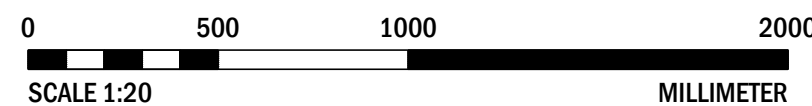[illegible]