




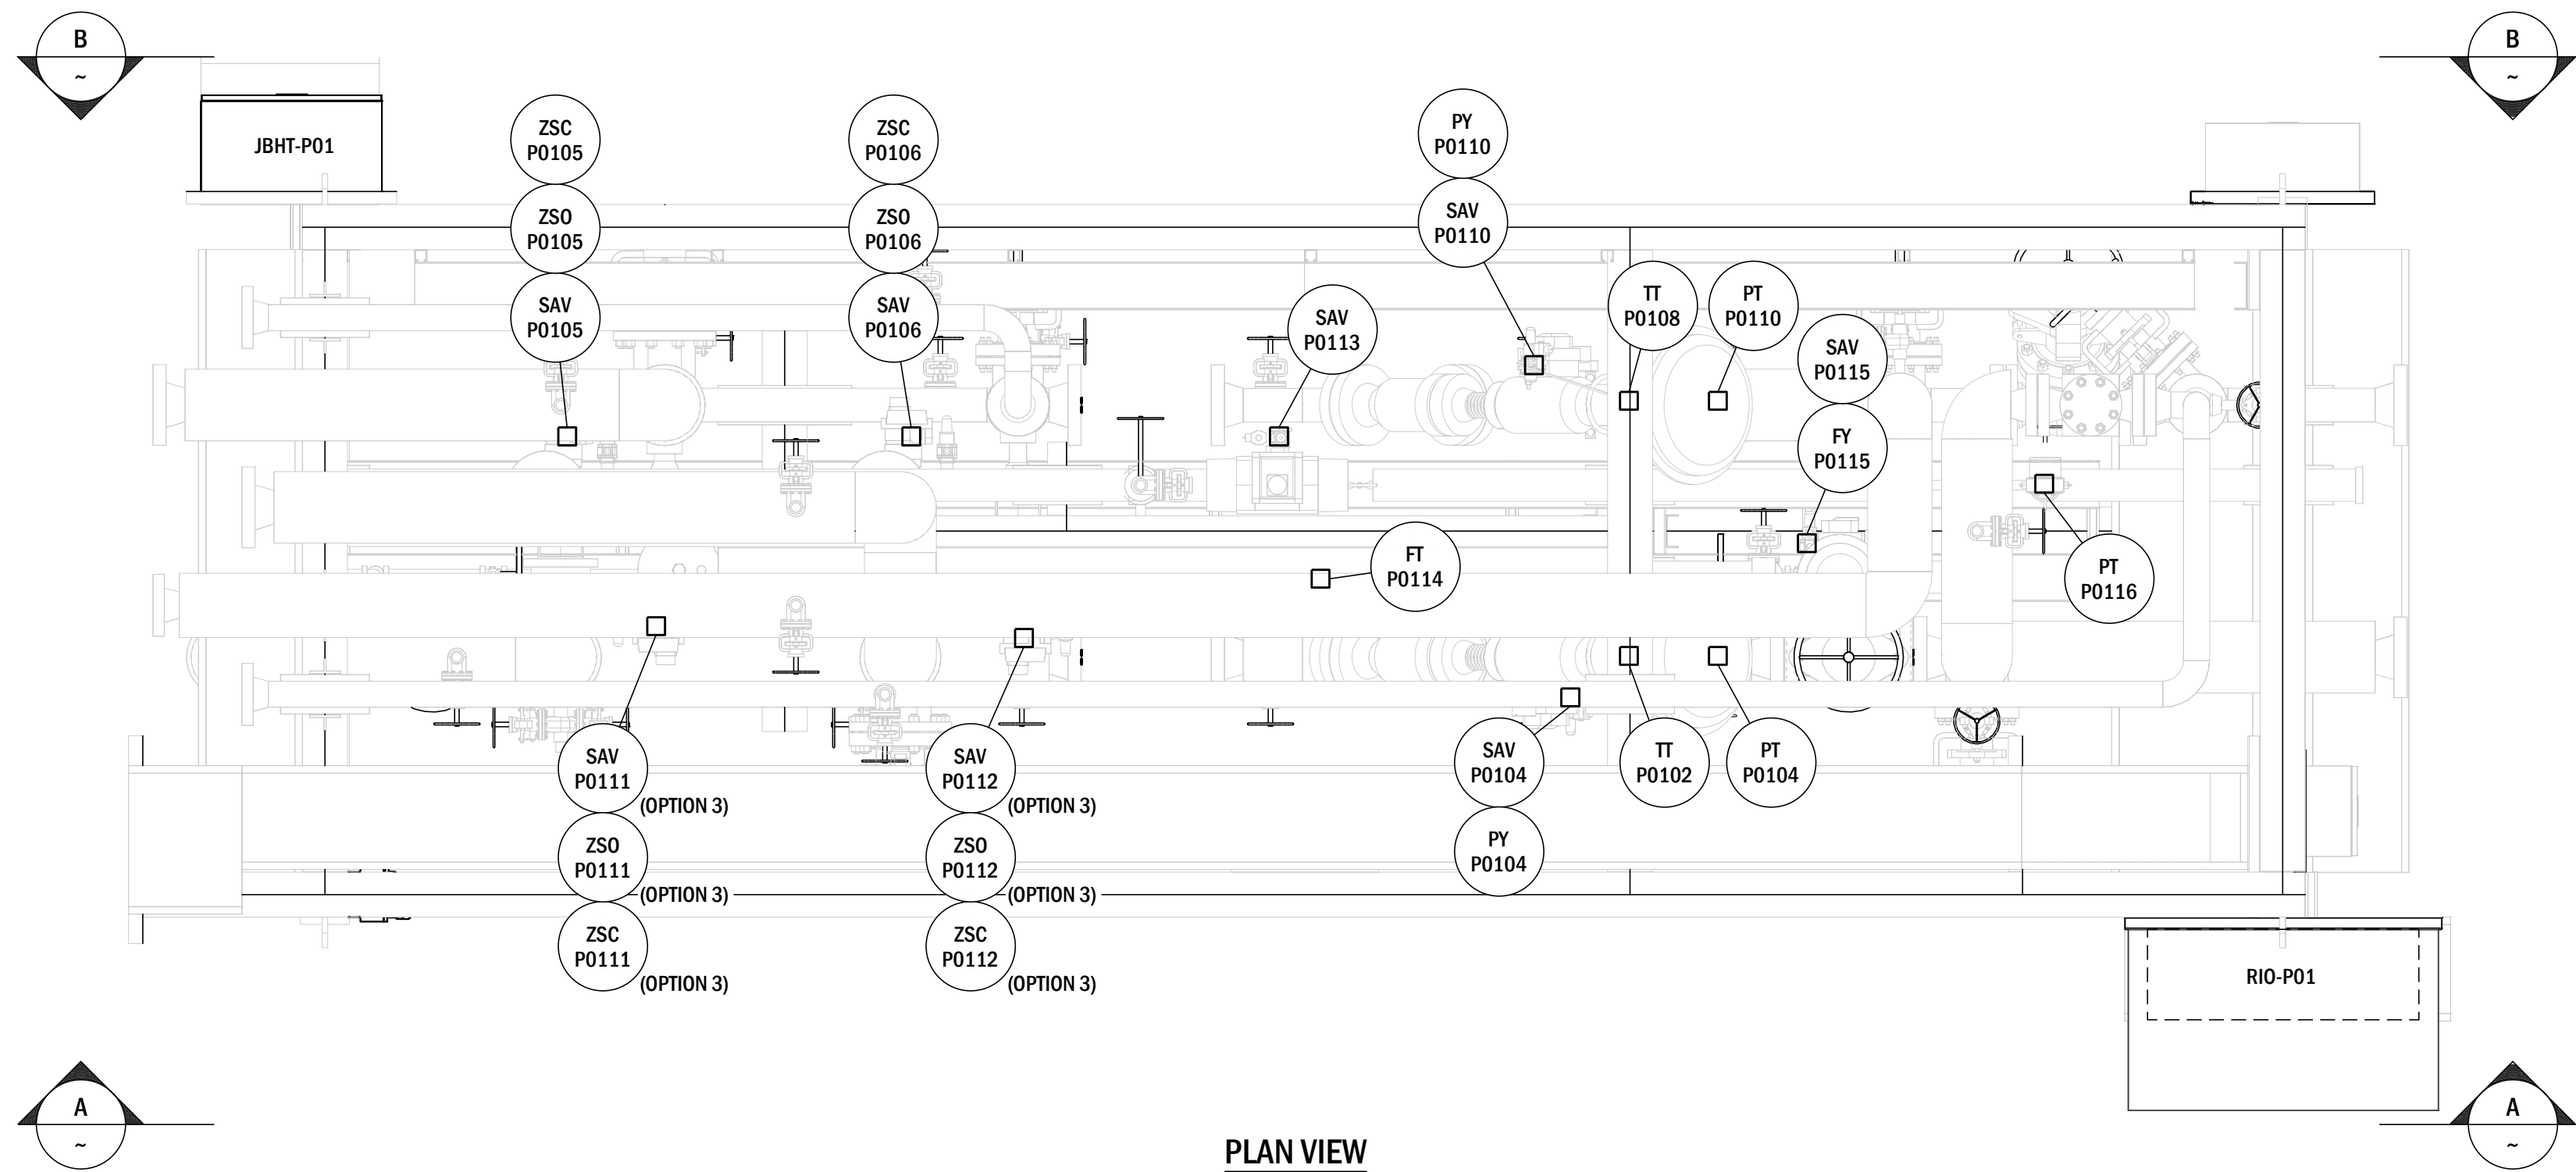

PLAN VIEW
SCALE: 1:20

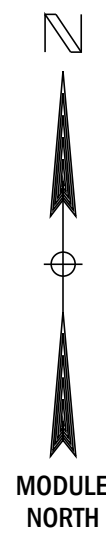

A
SECTION VIEW
SCALE 1:20

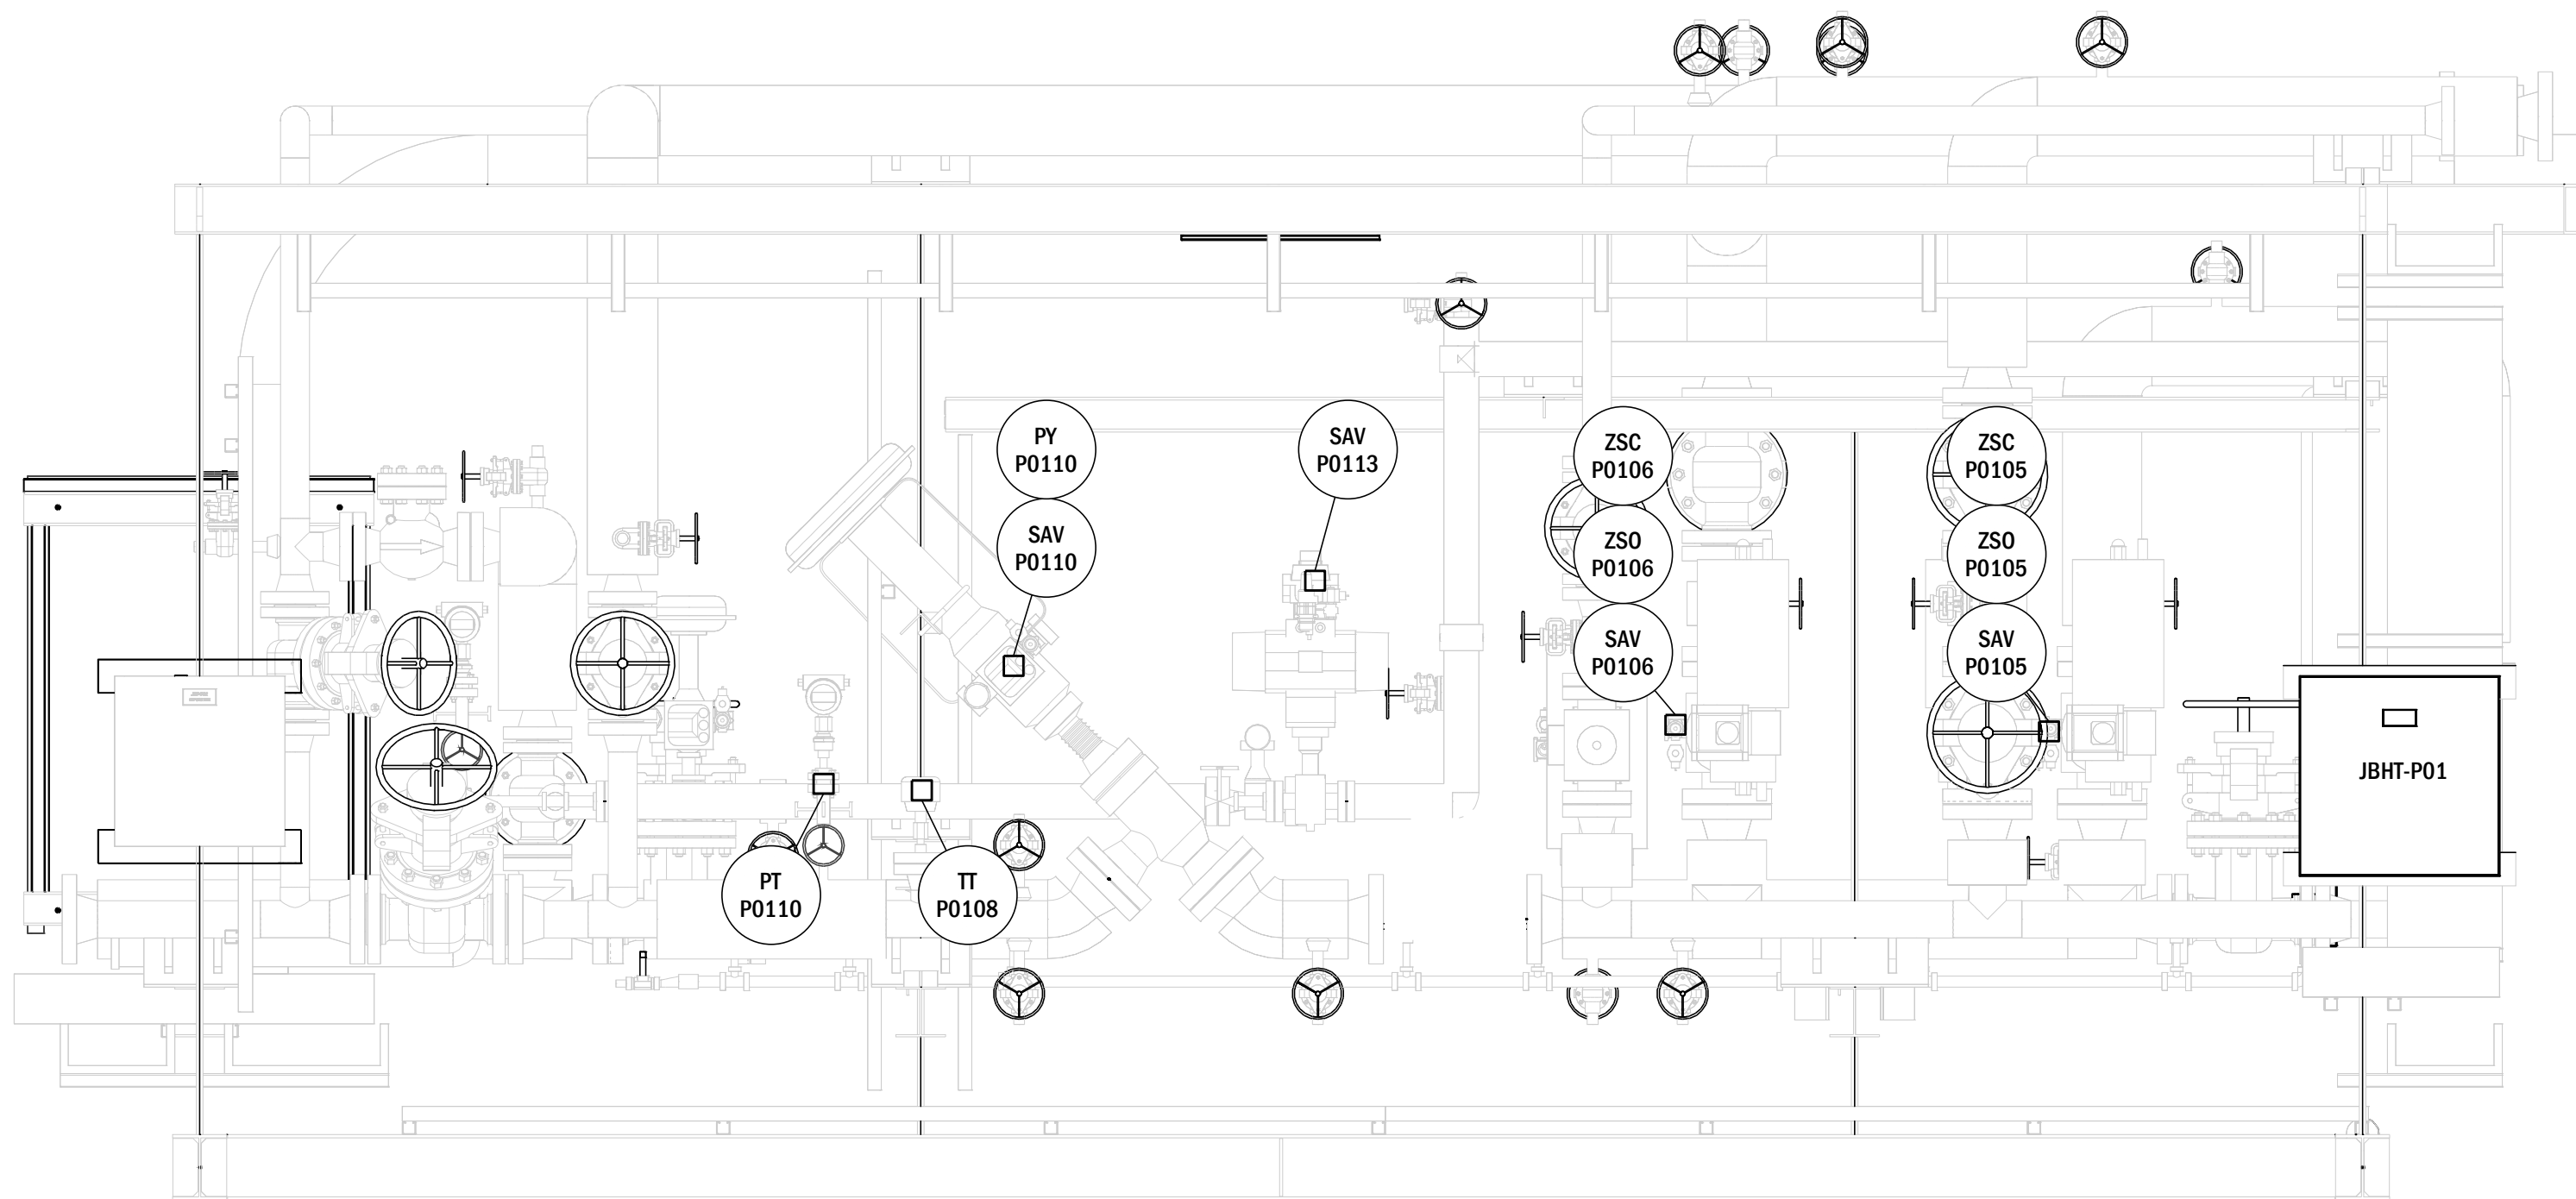

B
SECTION VIEW
SCALE 1:20

NOTES:

- FOR ELECTRICAL STANDARD INSTALLATION DETAILS, SEE E-STD-00-500-01 THRU 05 DRAWING SERIES.

SHOP NOTES:

- ALL ITEMS ON THIS MODULE (EXCLUDING MANUAL VALVES) INCLUDE THE TAG PREFIX PRD0154.

ENGINEERING NOTES:

- THIS DRAWING REFERENCES THE ENGINEERING RECORD G02-1-PRDXXX-E-GA-01-P01-02 REV 0 FOR ALL TECHNICAL INFORMATION. IN THE EVENT OF DISCREPANCY BETWEEN THIS DRAWING AND THE ENGINEERED DRAWING OF RECORD, THE ENGINEERED DRAWING OF RECORD WILL TAKE PRECEDENCE UNLESS THE CHANGE IS PROPERLY CLOUDED AS A REVISION TO THIS DRAWING AND STAMPED BY A PROFESSIONAL ENGINEER.

BASE
OPTION 3
OPTION 9

THIS MODULE IS TO BE LOCATED IN A ZONE 2 AREA,
GAS GROUP IIA AND SHALL BE WIRED ACCORDINGLY.
TEMPERATURE CODE IS T2D.
EQUIVALENT PROTECTION LEVELS Ga, Gb, Gc.
(FOR ELECTRICAL PURPOSES ONLY)

0 500 1000 2000
SCALE 1:20 MILLIMETER

SCOVAN INC.

2026.05.27

ISSUED FOR CONSTRUCTION

1 ISSUED FOR CONSTRUCTION WITH OPTION(S) 3, 9

0 ISSUED FOR CONSTRUCTION

2026.1111 2026.05.27 AUTO AUTO AUTO

2026.1111 2026.05.27 AUTO AUTO AUTO

JOB No. DATE BY CHK PE

PadX PARTNERSHIP

Scovan

PADX
NEXT GENERATION ENERGY SOLUTIONS
PRODUCTION MODULE (MOD-01-P01)
INSTRUMENTATION LAYOUT

CLIENT DRAWING NO.

DRAWING NO.

G02-1-PRD0154-E-GA-01-P01-02

REV.

1