
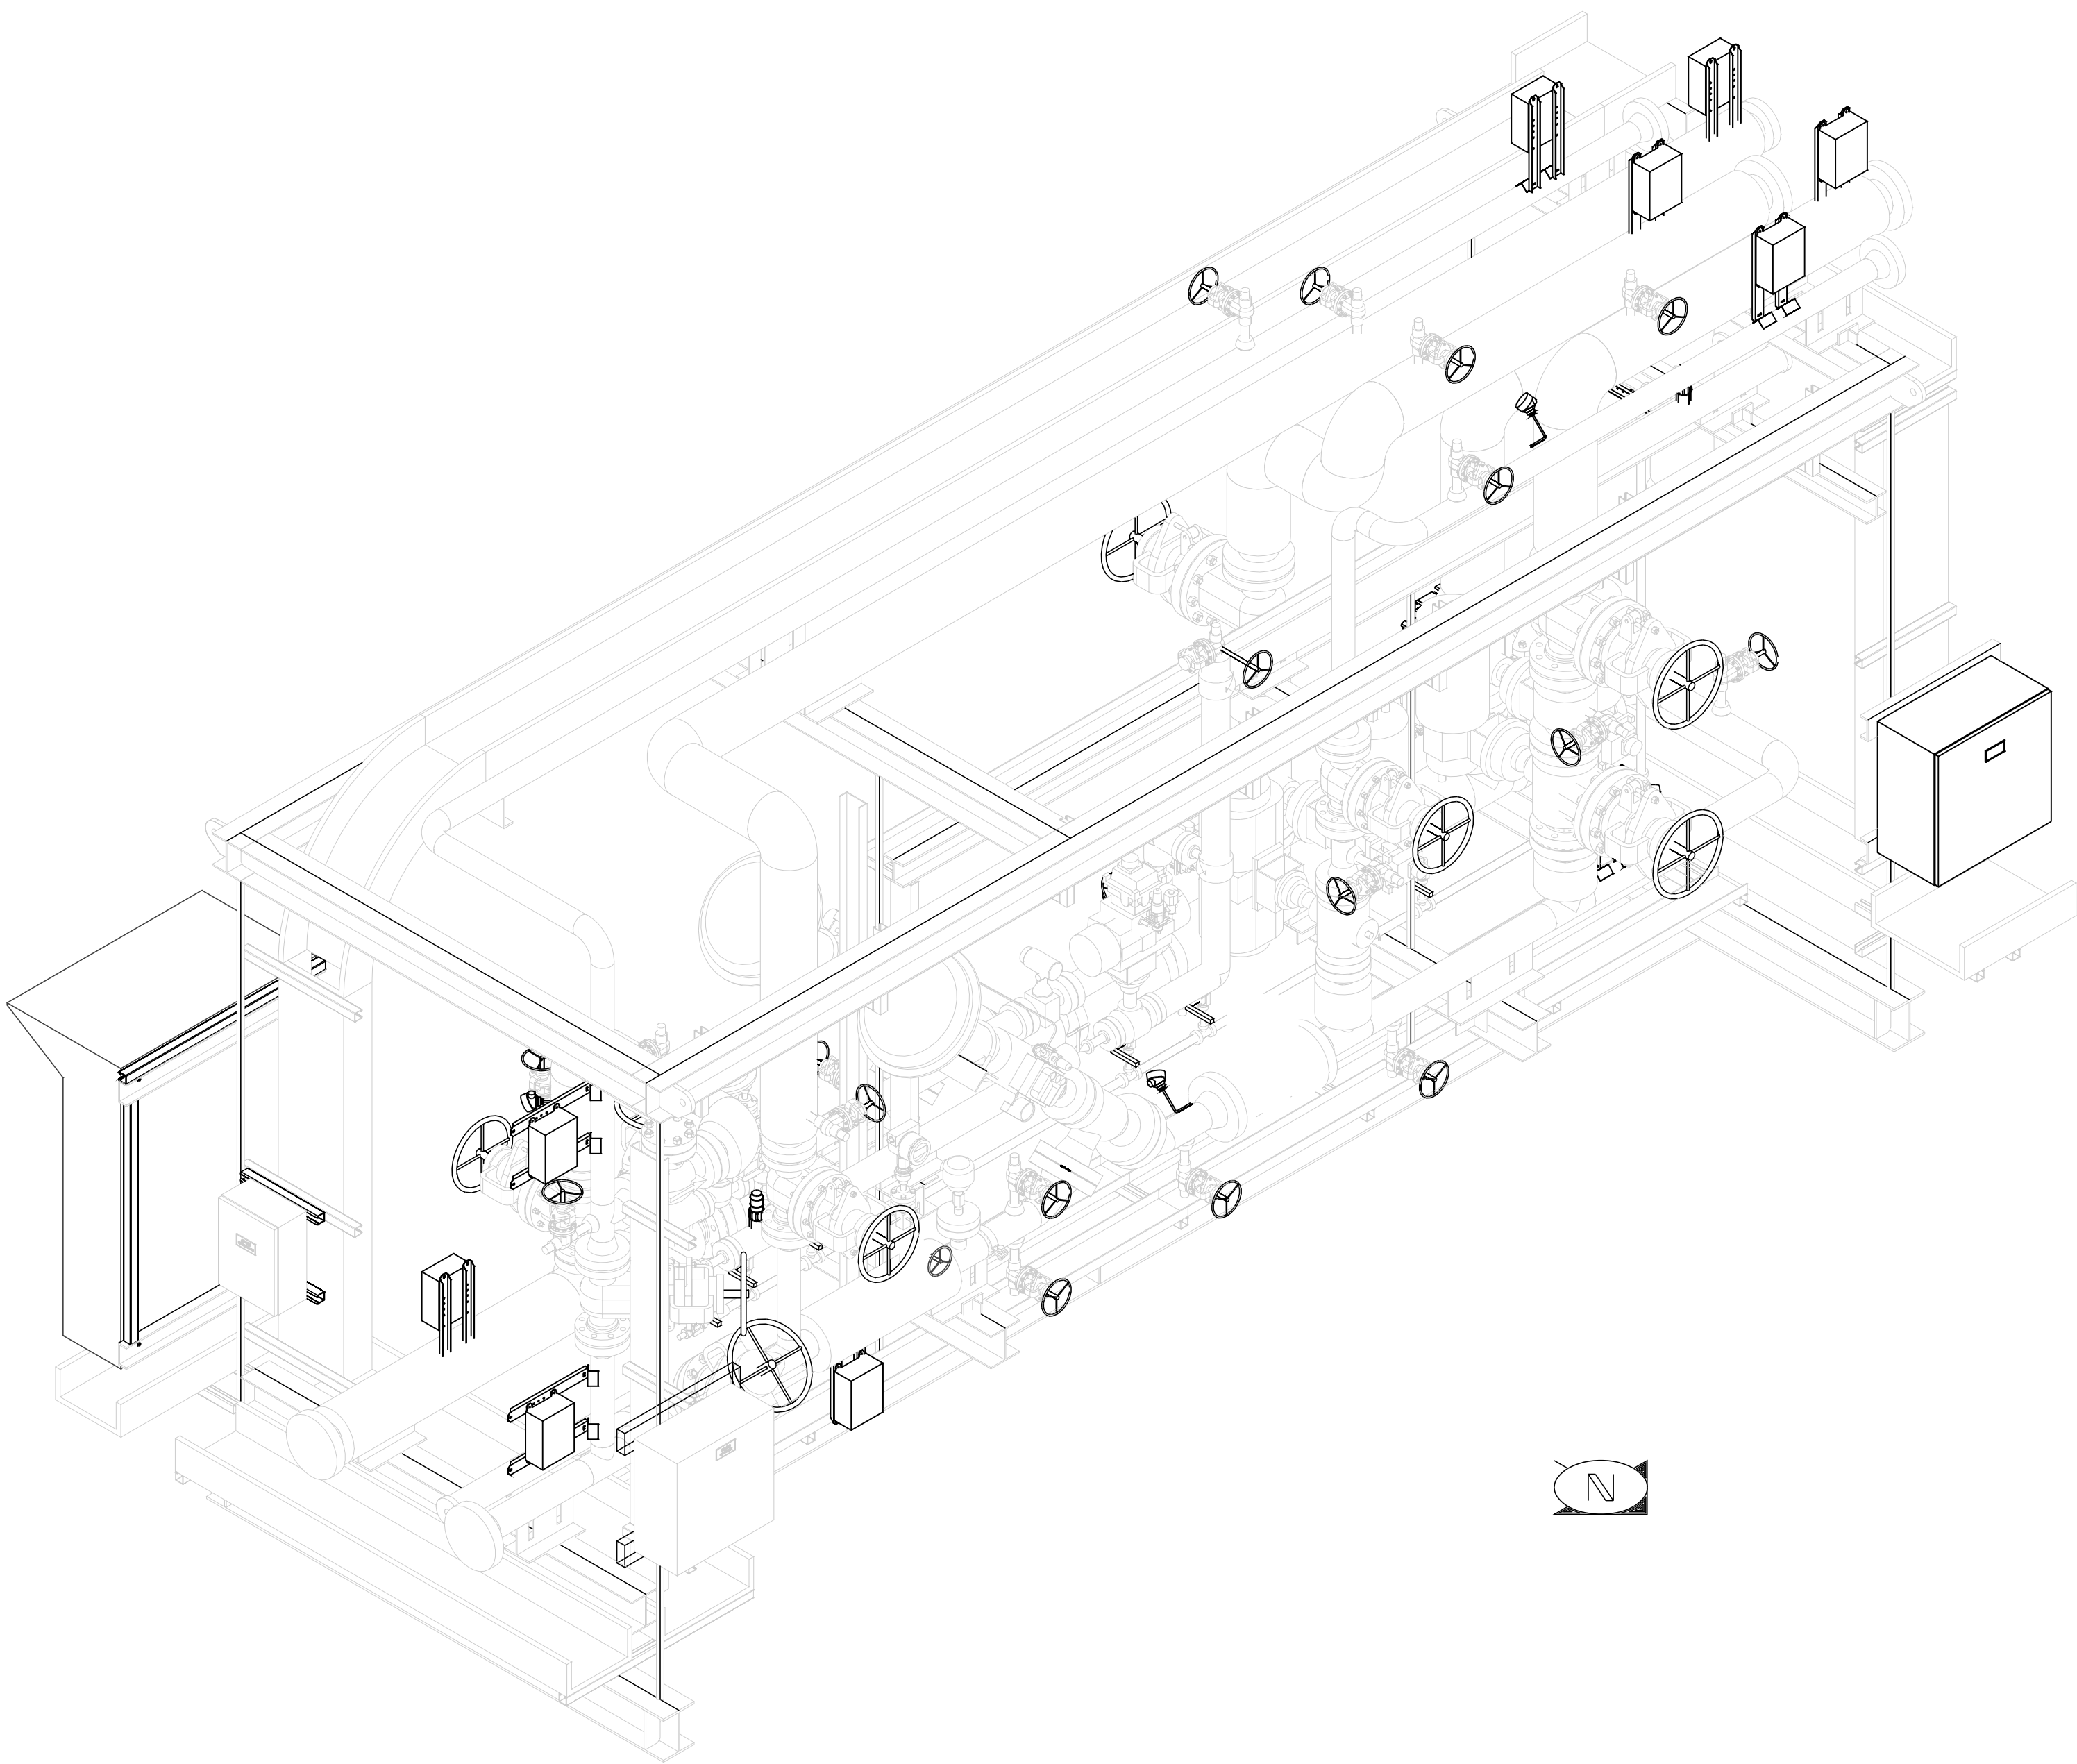


SHOP NOTES:

1. ALL ITEMS ON THIS MODULE (EXCLUDING MANUAL VALVES) INCLUDE THE TAG PREFIX PRD0154.

ENGINEERING NOTES:


1. THIS DRAWING REFERENCES THE ENGINEERING RECORD G02-1-PRDXXX-E-GA-01-P01-04 REV 0 FOR ALL TECHNICAL INFORMATION. IN THE EVENT OF DISCREPANCY BETWEEN THIS DRAWING AND THE ENGINEERED DRAWING OF RECORD, THE ENGINEERED DRAWING OF RECORD WILL TAKE PRECEDENCE UNLESS THE CHANGE IS PROPERLY CLOUDED AS A REVISION TO THIS DRAWING AND STAMPED BY A PROFESSIONAL ENGINEER.

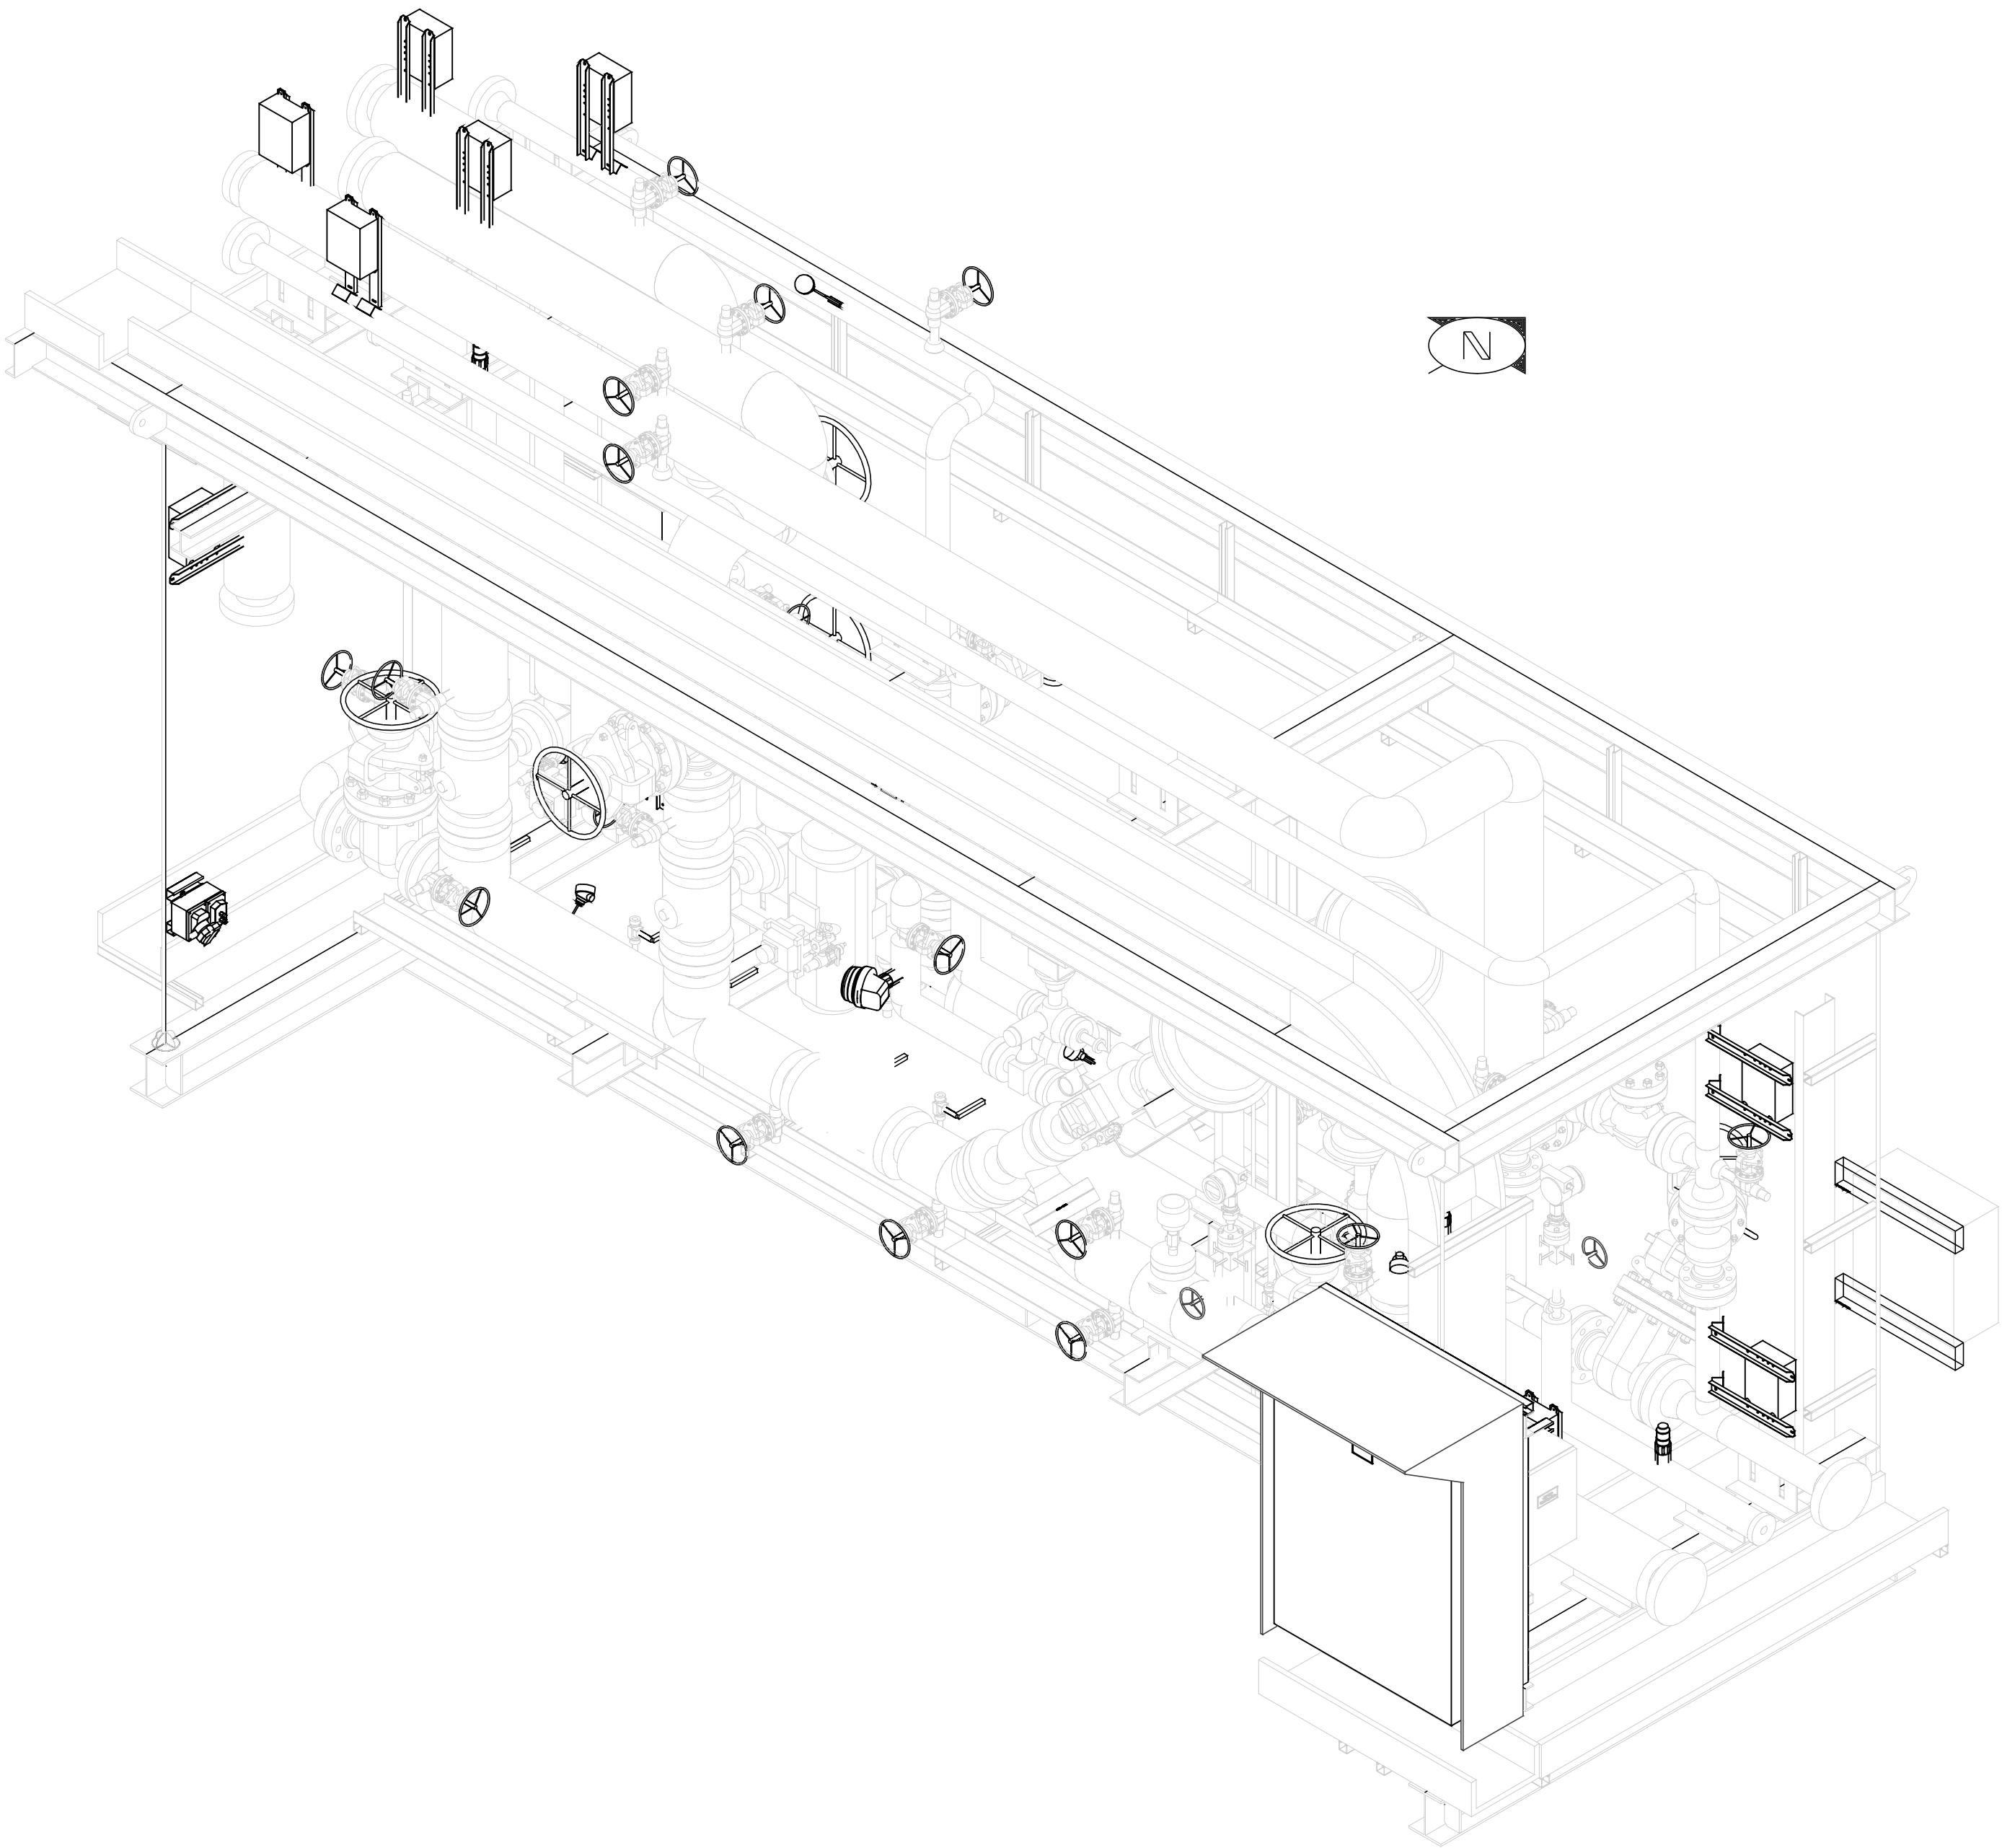

ISOMETRIC VIEW
SCALE : 1:20

BASE
OPTION 3
OPTION 9

THIS MODULE IS TO BE LOCATED IN A ZONE 2 AREA, GAS GROUP IIA AND SHALL BE WIRED ACCORDINGLY. TEMPERATURE CODE IS T2D. EQUIVALENT PROTECTION LEVELS Ga, Gb, Gc. (FOR ELECTRICAL PURPOSES ONLY)

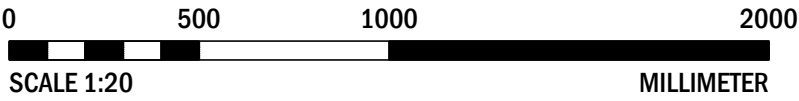

		SCOVAN INC. 2026.05.27 ISSUED FOR CONSTRUCTION										PadX PARTNERSHIP Scovan	PADX NEXT GENERATION ENERGY SOLUTIONS PRODUCTION MODULE (MOD-01-P01) ISOMETRIC LAYOUT		
			1	ISSUED FOR CONSTRUCTION WITH OPTION(S) 3, 9	2026.1111	2026.05.27	AUTO	AUTO	AUTO						
			0	ISSUED FOR CONSTRUCTION	2026.1111	2026.05.27	AUTO	AUTO	AUTO						
DRAWING NO.	REFERENCE DRAWINGS	STAMPS APPLY TO CURRENT REVISION ONLY		REV.	DESCRIPTION	JOB No.	DATE	BY	CHK	PE					