


JBHT-P01 - HEAT TRACE POWER & RTD JUNCTION BOX

M4

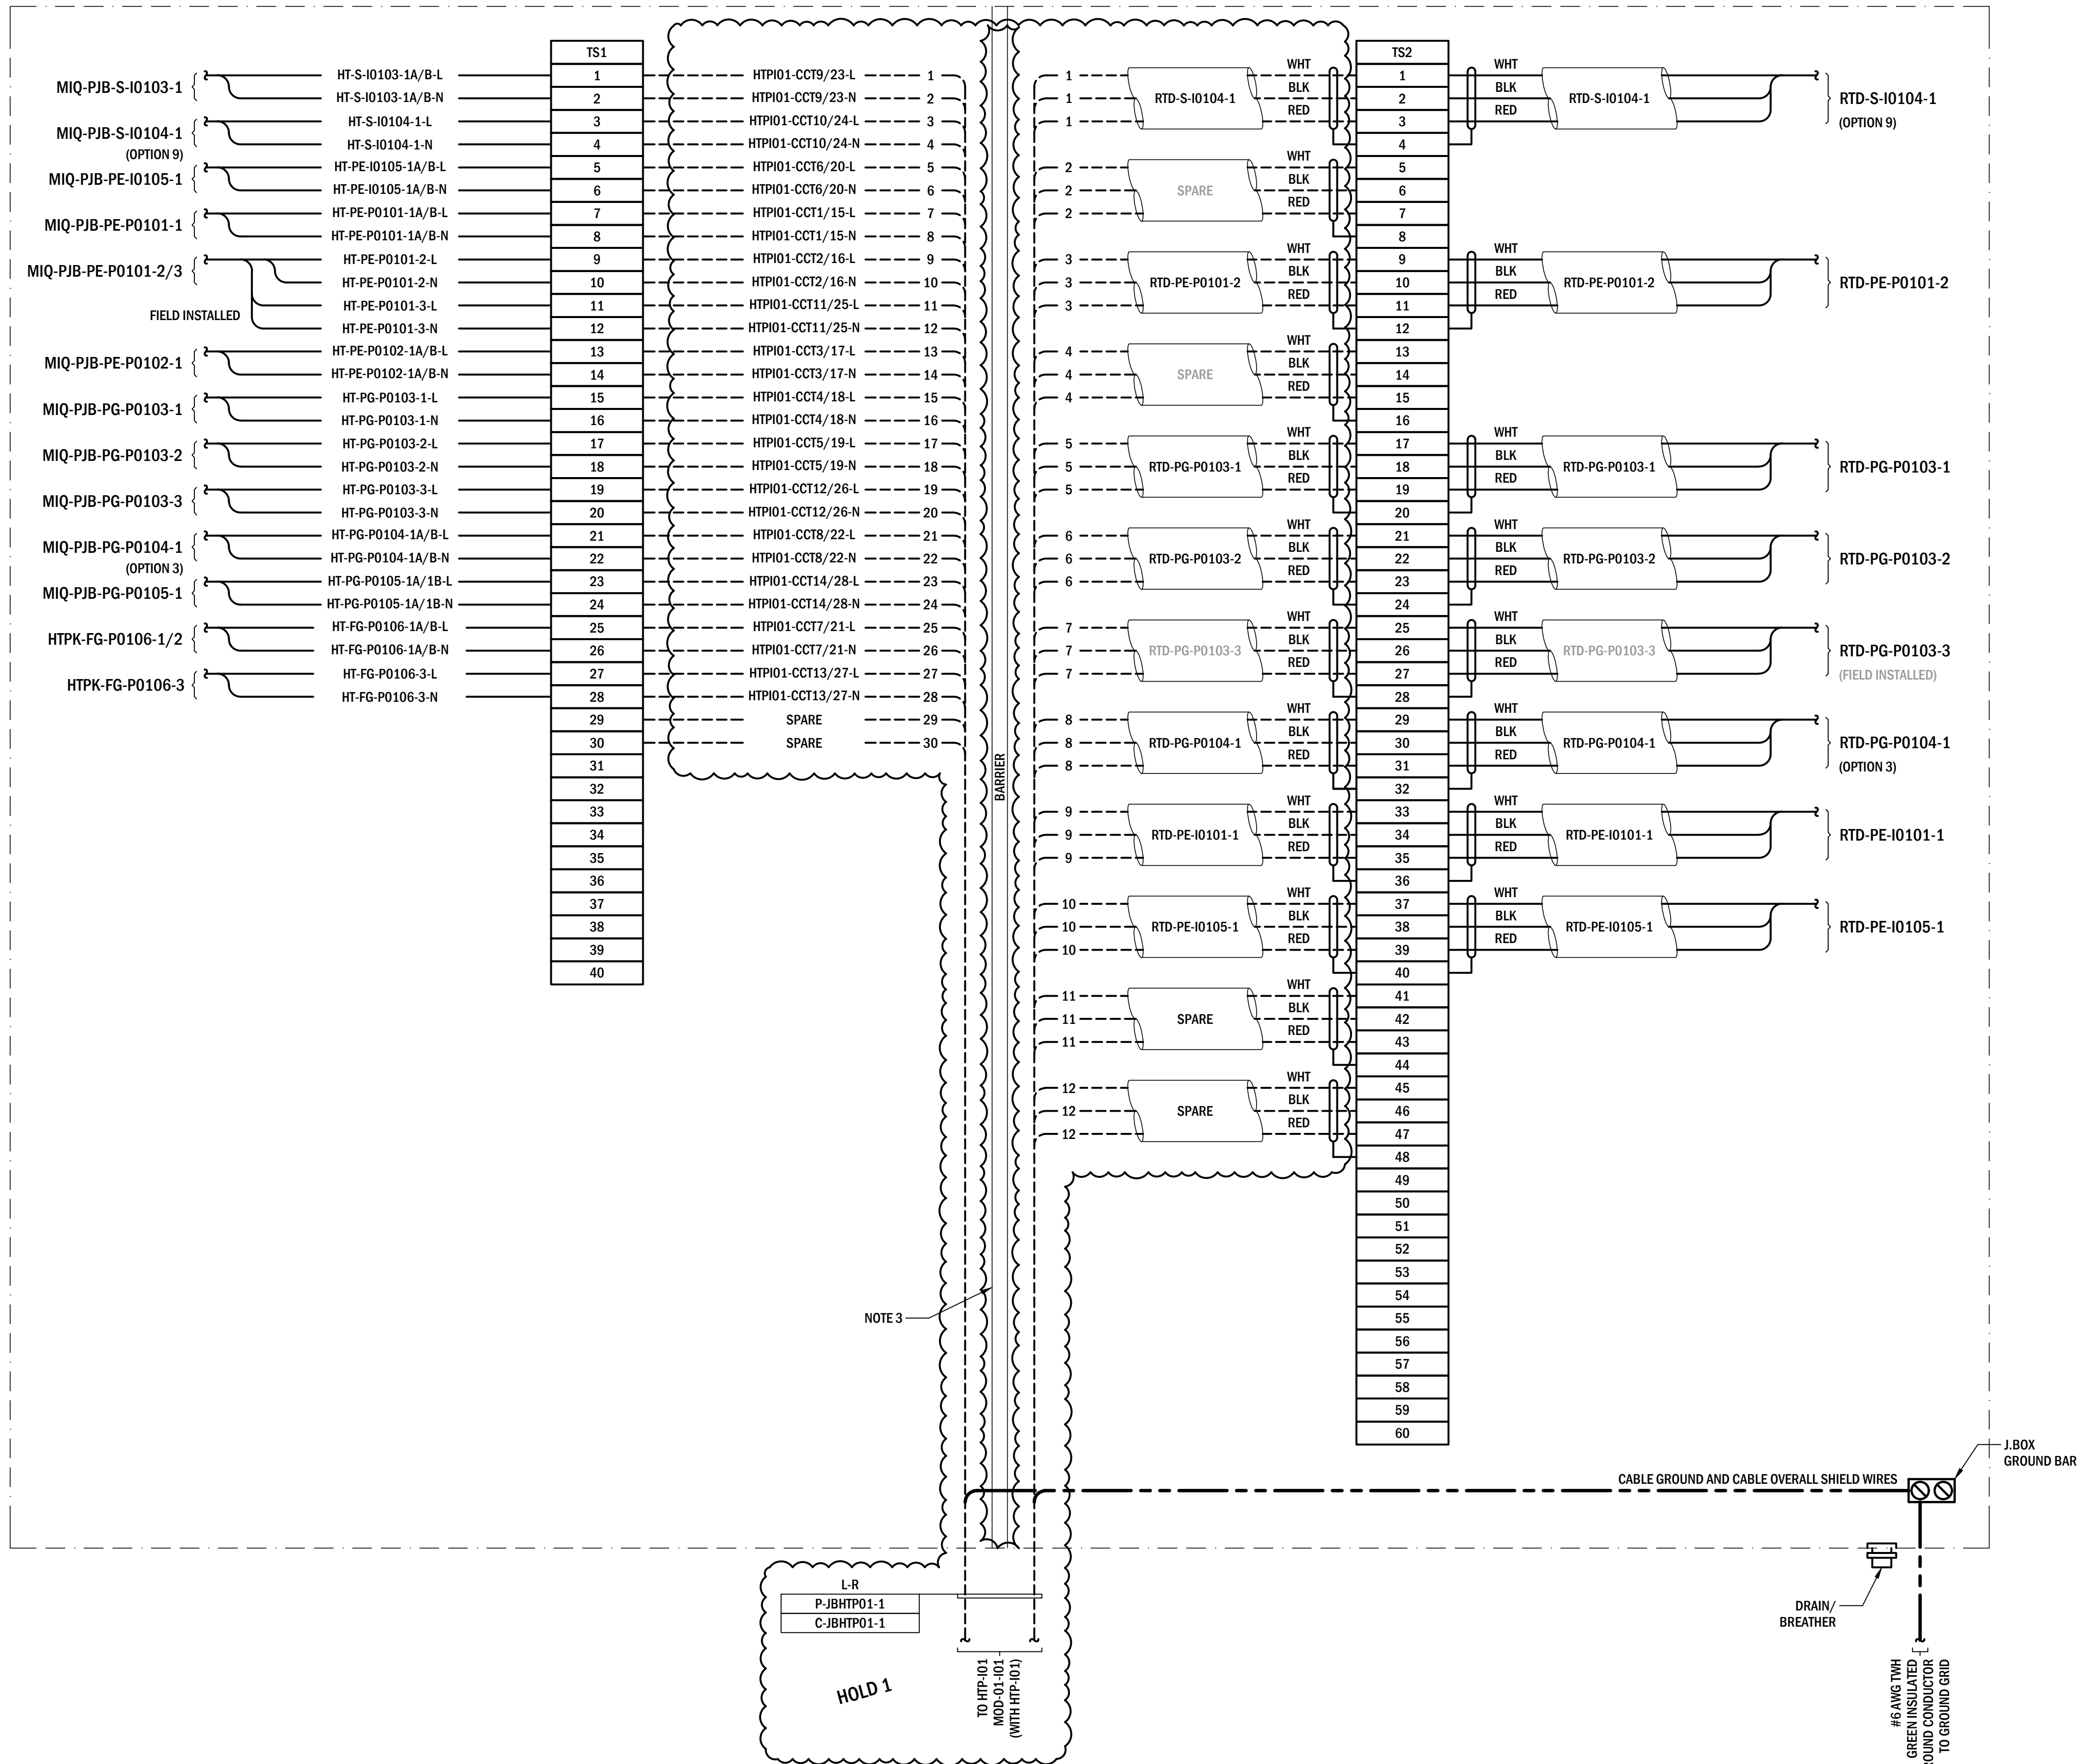

LAMICOID ENGRAVING DETAIL

(BLACK LETTERS ON WHITE BACKGROUND)


JBHT-P01
HEAT TRACE POWER & RTD
JUNCTION BOX

(WHITE LETTERS ON RED BACKGROUND)

CAUTION
MAY CONTAIN VOLTAGES
FROM MORE THAN
ONE SOURCE

NOTES:

- WIRING SIZES AND TYPE SHALL BE AS FOLLOWS (UNLESS OTHERWISE INDICATED):
 - EHT & POWER: 2c#10, 600 V, Cu
 - ANALOG: 1PR#16, 300 V, Cu, SHIELDED/
1TR#16, 300 V, Cu, SHIELDED
 - DISCRETE: 2c#14, 600 V, Cu
 - RTD: 1TR#18, 300 V, Cu, SHIELDED
- REFER TO DWG. E-STD-00-800-01 FOR JUNCTION BOX LAYOUT DETAIL.
- INSTALL WALL DIVIDER TO SEPARATE 120 VAC AND 24 VDC.
- JUNCTION BOX JBHT-P01 TO BE INSTALLED WITH DOOR SWING LEFT TO RIGHT. PLAN VIEW SHOWING ON THE DIAGRAM BELOW.

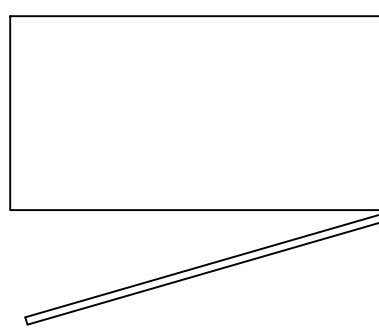

PLAN VIEW

SHOP NOTES:

- ALL ITEMS ON THIS MODULE (EXCLUDING MANUAL VALVES) INCLUDE THE TAG PREFIX PRD0154.

CONSTRUCTION NOTES:


- FIELD ELECTRICAL CONTRACTOR TO TERMINATE HOME RUN CABLE WITH FIRST CIRCUIT ON INS HTP-I01 OPTION AND SECOND CIRCUIT ON INS JBHT-I01.

HOLDS:

- FIELD RUN CABLE TO PRODUCTION MODULE HEAT TRACE JUNCTION BOX TO BE DETERMINED DURING SITE SPECIFIC ENGINEERING.

ENGINEERING NOTES:

- THIS DRAWING REFERENCES THE ENGINEERING RECORD G02-1-PRDXXX E-JB-01-P01-01 REV 0 FOR ALL TECHNICAL INFORMATION. IN THE EVENT OF DISCREPANCY BETWEEN THIS DRAWING AND THE ENGINEERED DRAWING OF RECORD, THE ENGINEERED DRAWING OF RECORD WILL TAKE PRECEDENCE UNLESS THE CHANGE IS PROPERLY CLOUDED AS A REVISION TO THIS DRAWING AND STAMPED BY A PROFESSIONAL ENGINEER.

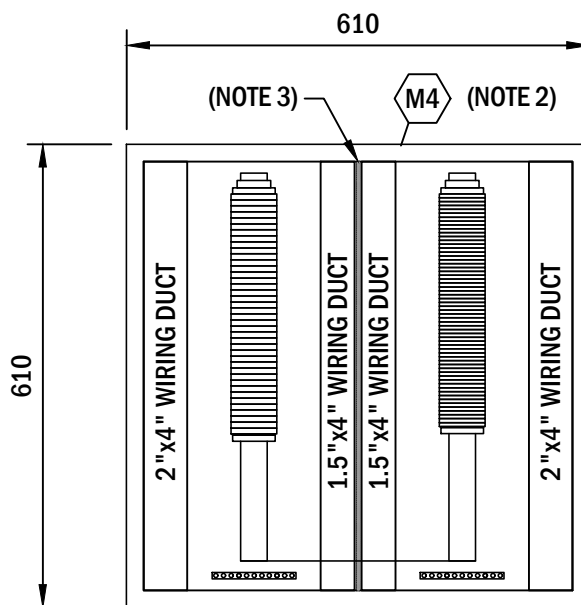JUNCTION BOX DETAIL
SCALE 1:10

SCOVAN INC.

2026.05.26

ISSUED FOR CONSTRUCTION

1 ISSUED FOR CONSTRUCTION WITH OPTION(S) 3, 9

2026.1111

2026.05.26

AUTO

AUTO

AUTO

0 ISSUED FOR CONSTRUCTION

2026.1111

2026.05.26

AUTO

AUTO

AUTO

DRAWING NO. REFERENCE DRAWINGS

STAMPS APPLY TO CURRENT REVISION ONLY

PLOTTED BY: ACESUSER

Plot Date: May, 26 @ 06:47 PM

THIS DOCUMENT'S USE IS CONDITIONED UPON THE USER'S AGREEMENT NOT TO USE, DISCLOSE OR OTHERWISE DISSEMINATE DOCUMENT, IN WHOLE OR IN PART, FOR ANY PURPOSE EXCEPT AS SPECIFICALLY INTENDED BY SCOVAN INC. ANY PRINTED VERSION OF THIS DOCUMENT IS A COPY AND IS NOT A REPRESENTATION OF THE ORIGINALLY AUTHENTICATED DOCUMENT.

PadX PARTNERSHIP

Scovan

PADX
NEXT GENERATION ENERGY SOLUTIONS
PRODUCTION MODULE (MOD-01-P01)
JUNCTION BOX JBHT-P01 WIRING DIAGRAM

CLIENT DRAWING NO.

DRAWING NO.

G02-1-PRD0154-E-JB-01-P01-01

REV.

1