




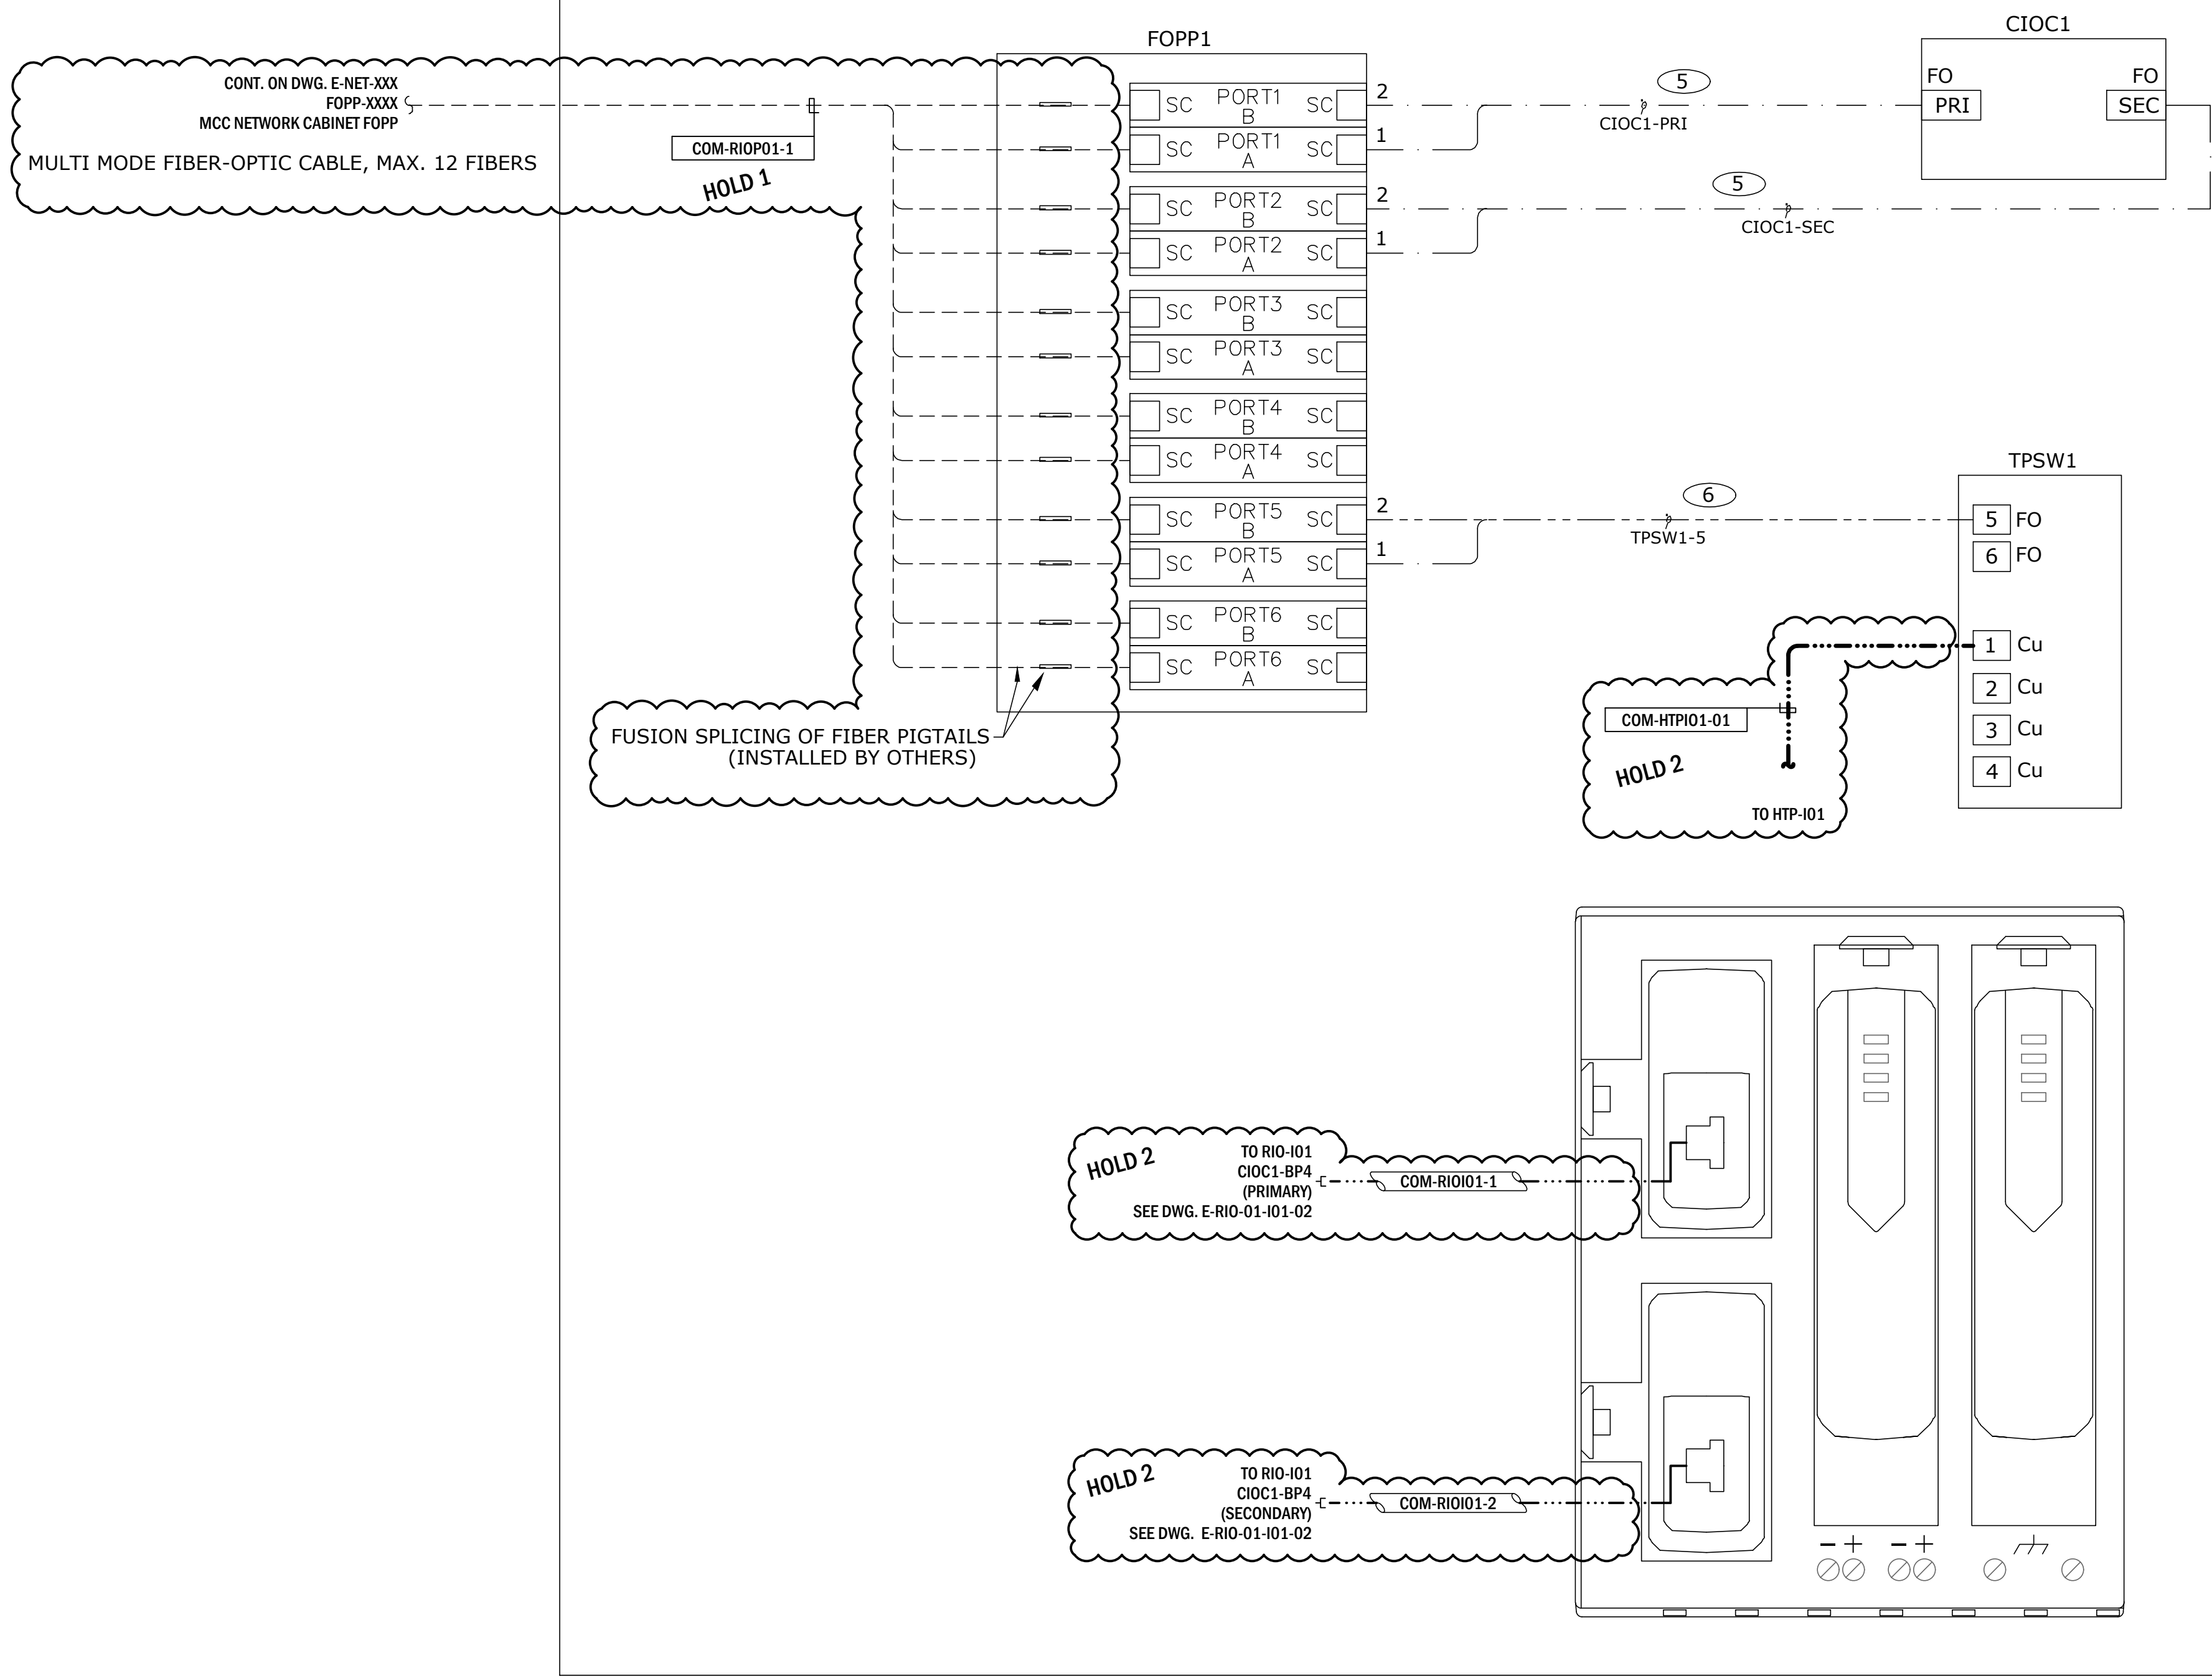


CIOC FIBER CONNECTION DETAIL

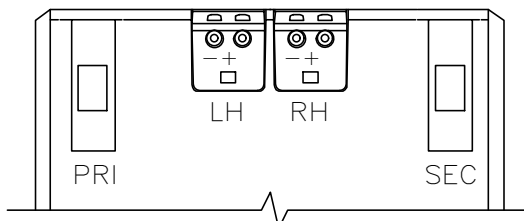

CHARM IO BLOCK DETAIL

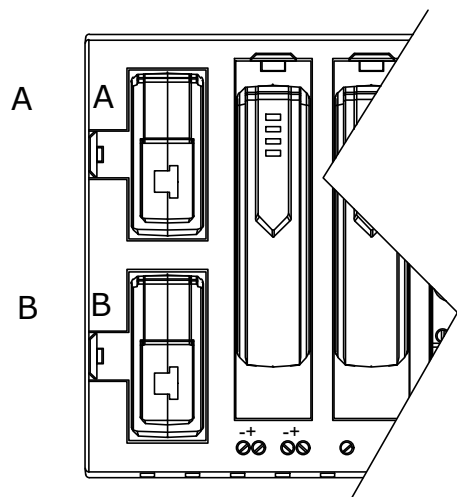

CHARM GATEWAY DETAIL

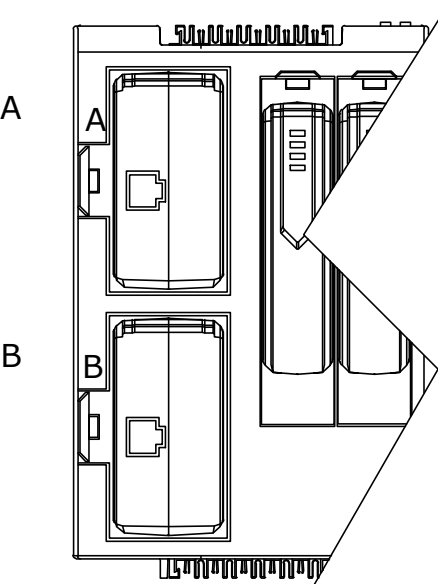

HOLDS:

- PANEL INCOMING FIBER CABLE OPTICS CABLE TO BE DETERMINED DURING SITE SPECIFIC ENGINEERING.
- CAT6 ETHERNET CABLE TO BE DETERMINED DURING SITE SPECIFIC ENGINEERING.

SHOP NOTES:

- ALL ITEMS ON THIS MODULE (EXCLUDING MANUAL VALVES) INCLUDE THE TAG PREFIX PRD0154.

ENGINEERING NOTES:

- THIS DRAWING REFERENCES THE ENGINEERING RECORD G02-1-PRDXXX-E-RIO-01-P01-12 REV 0 FOR ALL TECHNICAL INFORMATION. IN THE EVENT OF DISCREPANCY BETWEEN THIS DRAWING AND THE ENGINEERED DRAWING OF RECORD, THE ENGINEERED DRAWING OF RECORD WILL TAKE PRECEDENCE UNLESS THE CHANGE IS PROPERLY CLOUDED AS A REVISION TO THIS DRAWING AND STAMPED BY A PROFESSIONAL ENGINEER.

LEGEND:

- FIBER OPTICAL PATCH CORD
- DELTAV PRIMARY
- DELTAV SECONDARY

NOTE:

- 1 INSTALLED AND SUPPLIED BY OTHERS

REDRAWN FROM SPARTAN
VENDOR DRAWING PACKAGE
DV-54809-ZX-700-00 REV 0

		SCOVAN INC. 2026.05.26 ISSUED FOR CONSTRUCTION										PadX PARTNERSHIP Scovan	PADX NEXT GENERATION ENERGY SOLUTIONS PRODUCTION MODULE (MOD-01-P01) REMOTE I/O PANEL RIO-P01 NETWORK COMMUNICATION DETAILS		
DRAWING NO.	REFERENCE DRAWINGS		STAMPS APPLY TO CURRENT REVISION ONLY		REV.	DESCRIPTION	JOB No.	DATE	BY	CHK	PE		CLIENT DRAWING NO.	DRAWING NO.	REV.
				1	ISSUED FOR CONSTRUCTION WITH OPTION(S) 3, 9	2026.1111	2026.05.26	AUTO	AUTO	AUTO	-	G02-1-PRD0154-E-RIO-01-P01-12	1		
				0	ISSUED FOR CONSTRUCTION	2026.1111	2026.05.26	AUTO	AUTO	AUTO					