


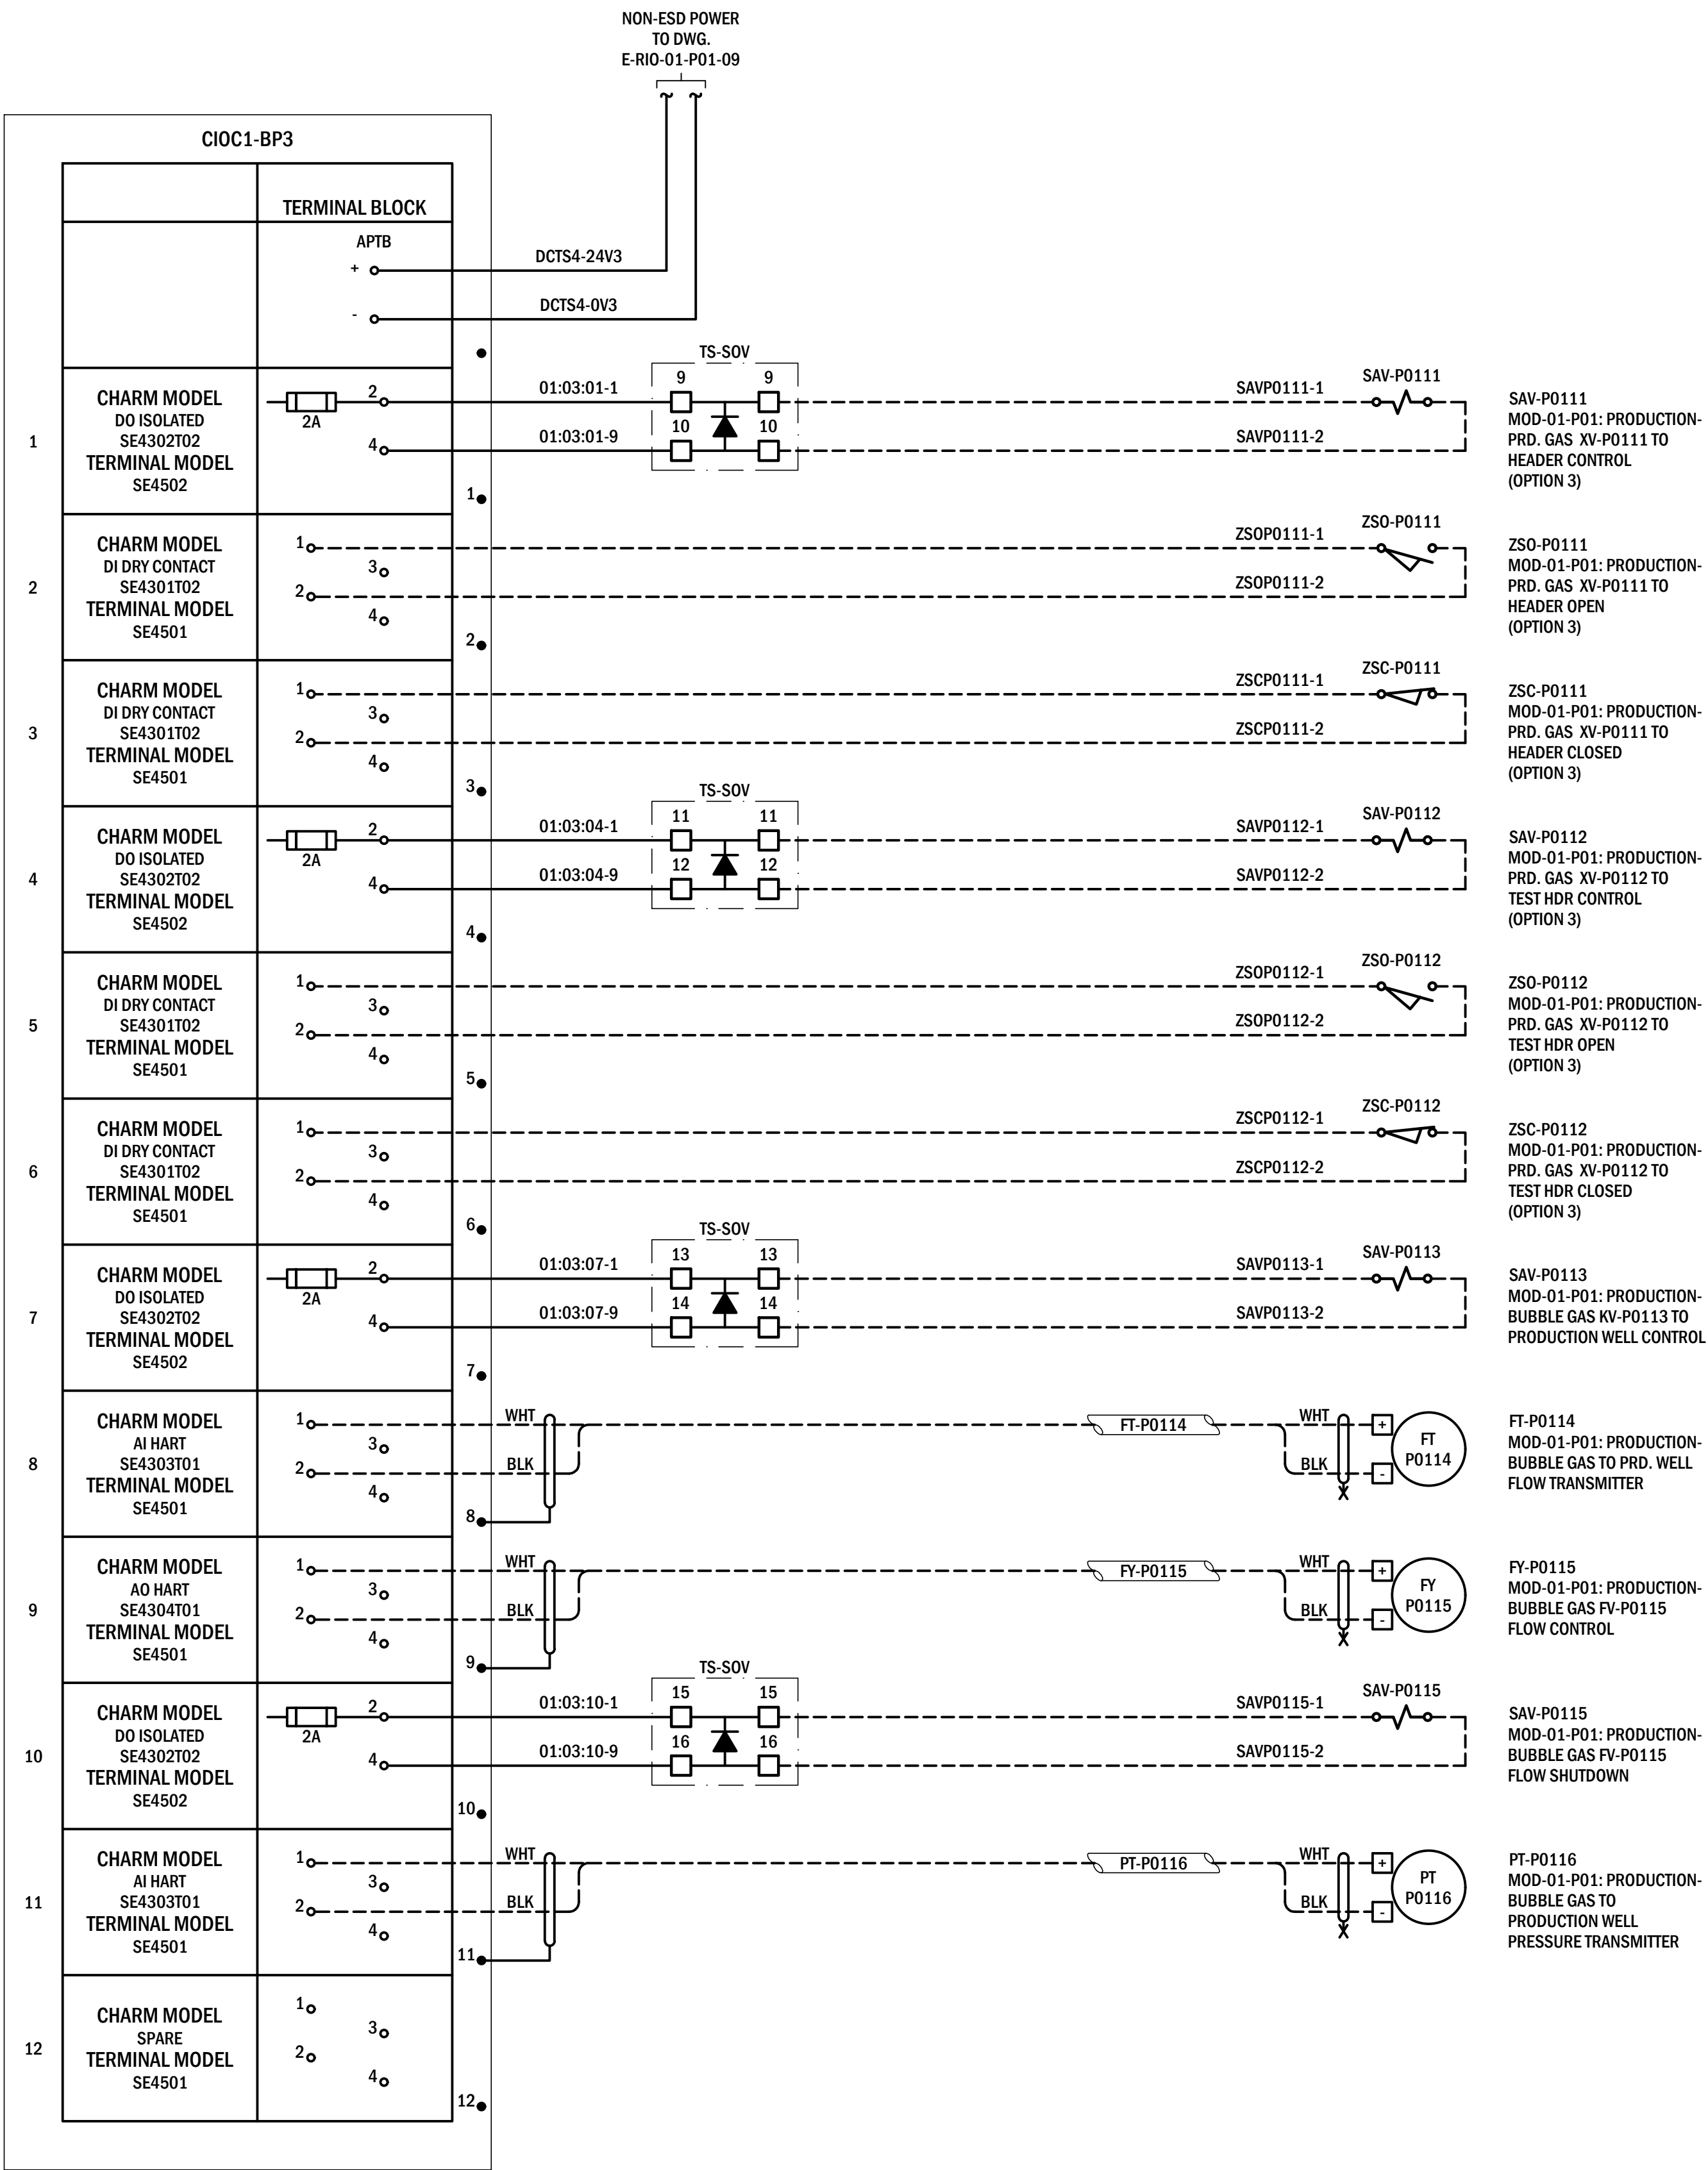

- TERMINAL LEGEND**
- CONTROL PANEL**
- FUSED TERMINAL c/w LED & GROUND TERMINAL
 - DISCONNECT TERMINAL
 - FEED THROUGH TERMINAL
 - MCC TERMINAL
 - CONTACTOR PANEL TERMINAL
 - VENDOR TERMINAL
 - FIELD JUNCTION BOX TERMINAL

- SHOP NOTES:**
- ALL ITEMS ON THIS MODULE (EXCLUDING MANUAL VALVES) INCLUDE THE TAG PREFIX PRD0154.
- ENGINEERING NOTES:**
- THIS DRAWING REFERENCES THE ENGINEERING RECORD G02-1-PRDXXX-E-RIO-01-P01-14 REV 0 FOR ALL TECHNICAL INFORMATION. IN THE EVENT OF DISCREPANCY BETWEEN THIS DRAWING AND THE ENGINEERED DRAWING OF RECORD, THE ENGINEERED DRAWING OF RECORD WILL TAKE PRECEDENCE UNLESS THE CHANGE IS PROPERLY CLOUDDED AS A REVISION TO THIS DRAWING AND STAMPED BY A PROFESSIONAL ENGINEER.

BASE
OPTION 3