


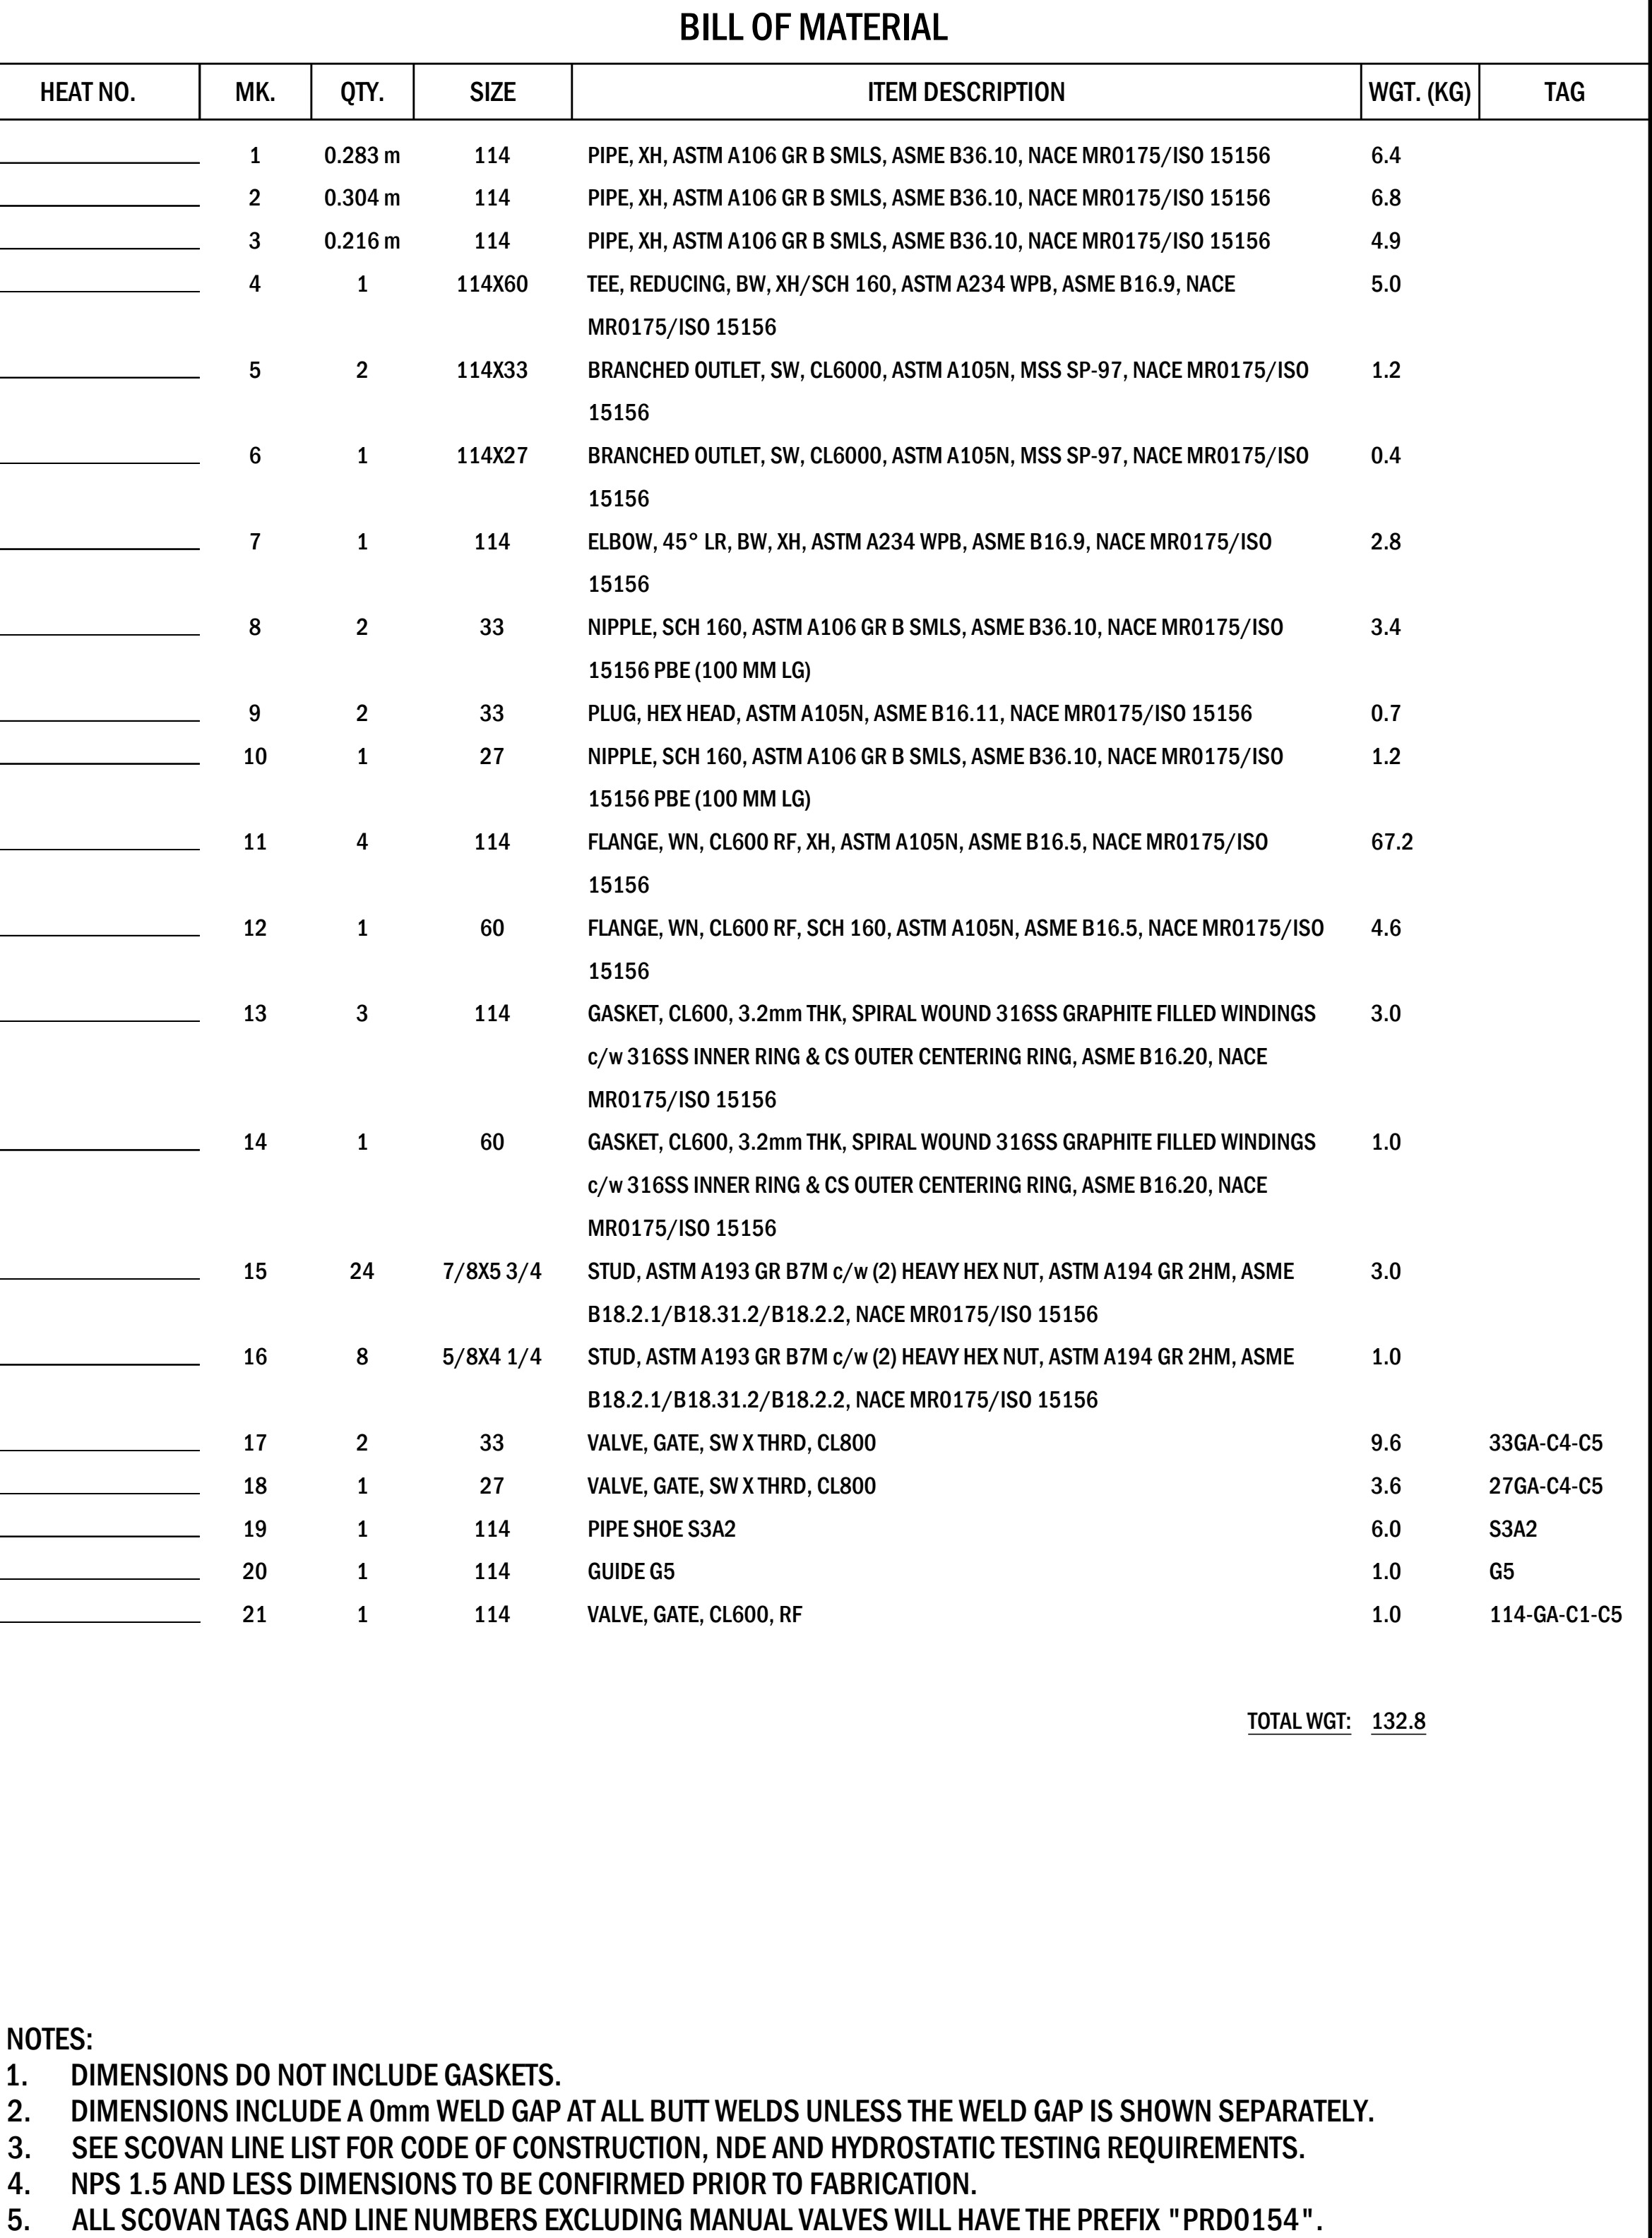

MK.	TYPE	WELDER	WPS	DATE	MK.	TYPE	WELDER	WPS	DATE	MK.	TYPE	WELDER	WPS	DATE	MK.	TYPE	WELDER	WPS	DATE	CN.	MOD. NO.	WPS.			
A	BW				F	OLET				K	BW				P	BW				007		SCO-022-P1 R.3			
B	BW				G	SW				L	OLET				Q	BW				INSULATION	64H	PAINT -			
C	OLET				H	SW				M	SW									LINE NO.	114-PE-C1C5-P0101				
D	SW				I	BW				N	SW									CLIENT DRAWING NO.	-				
E	SW				J	BW				O	BW														
						SCOVAN INC. 2026.05.26 ISSUED FOR CONSTRUCTION														PadX PARTNERSHIP Scovan		PADX NEXT GENERATION ENERGY SOLUTIONS PRODUCTION MODULE (MOD-01-P01) PIPING ISOMETRIC DRAWING			
										1	ISSUED FOR CONSTRUCTION WITH OPTION(S) 3, 9				2026.1111	2026.05.26	AUTO	AUTO	AUTO						
										0	ISSUED FOR CONSTRUCTION				2026.1111	2026.05.26	AUTO	AUTO	AUTO						
DRAWING NO.		REFERENCE DRAWINGS								STAMPS APPLY TO CURRENT REVISION ONLY				REV.	DESCRIPTION				JOB No.	DATE	BY	CHK	PE	CLIENT DRAWING NO.	DRAWING NO.
																					G02-1-PRD0154-M-MSP-01-P01-P0101-02		1		