


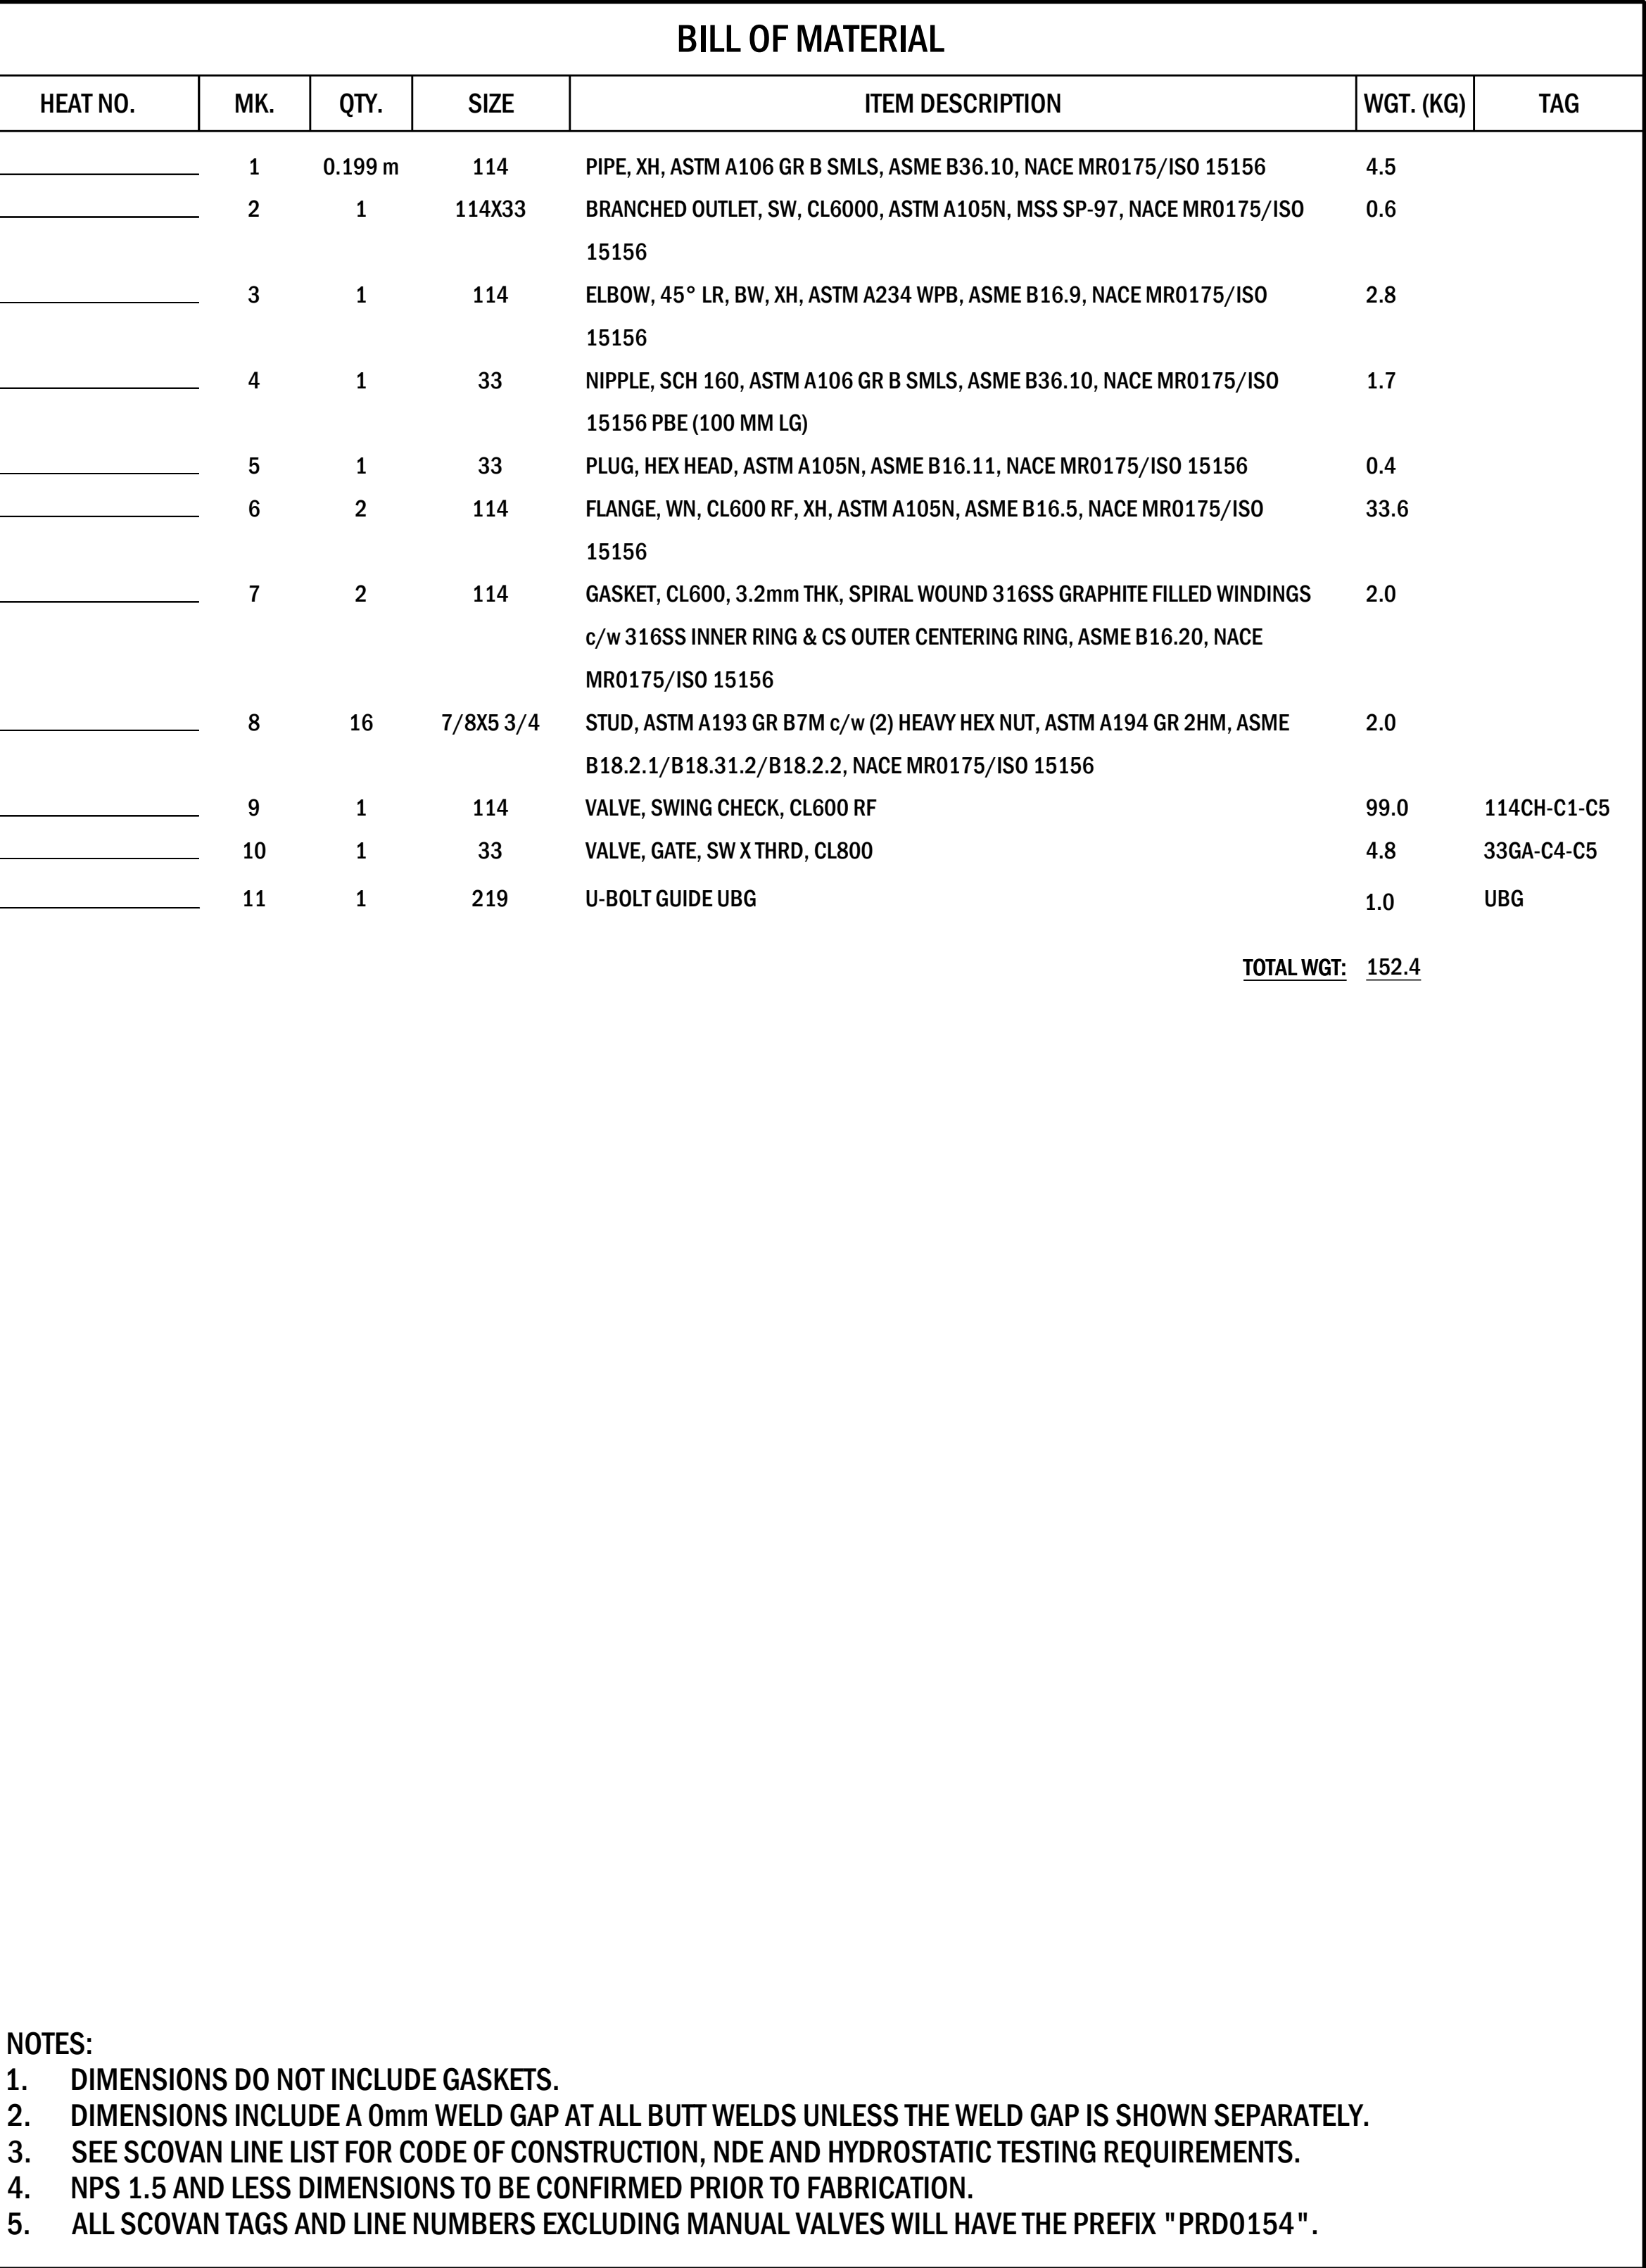

WELD MAP - SHOP USE ONLY																														
MK.	TYPE	WELDER	WPS	DATE	MK.	TYPE	WELDER	WPS	DATE	MK.	TYPE	WELDER	WPS	DATE	MK.	TYPE	WELDER	WPS	DATE	MK.	TYPE	WELDER	WPS	DATE						
A	BW				F	BW																								
B	OLET																													
C	SW																													
D	SW																													
E	BW																													
					SCOVAN INC. 2026.05.26 ISSUED FOR CONSTRUCTION																PadX PARTNERSHIP Scovan		PADX NEXT GENERATION ENERGY SOLUTIONS PRODUCTION MODULE (MOD-01-P01) PIPING ISOMETRIC DRAWING CLIENT DRAWING NO. DRAWING NO. G02-1-PRD0154-M-MSP-01-P01-P0103-03							
DRAWING NO.		REFERENCE DRAWINGS			STAMPS APPLY TO CURRENT REVISION ONLY									REV.	DESCRIPTION							JOB No.	DATE	BY	CHK	PE	REV. 1			