


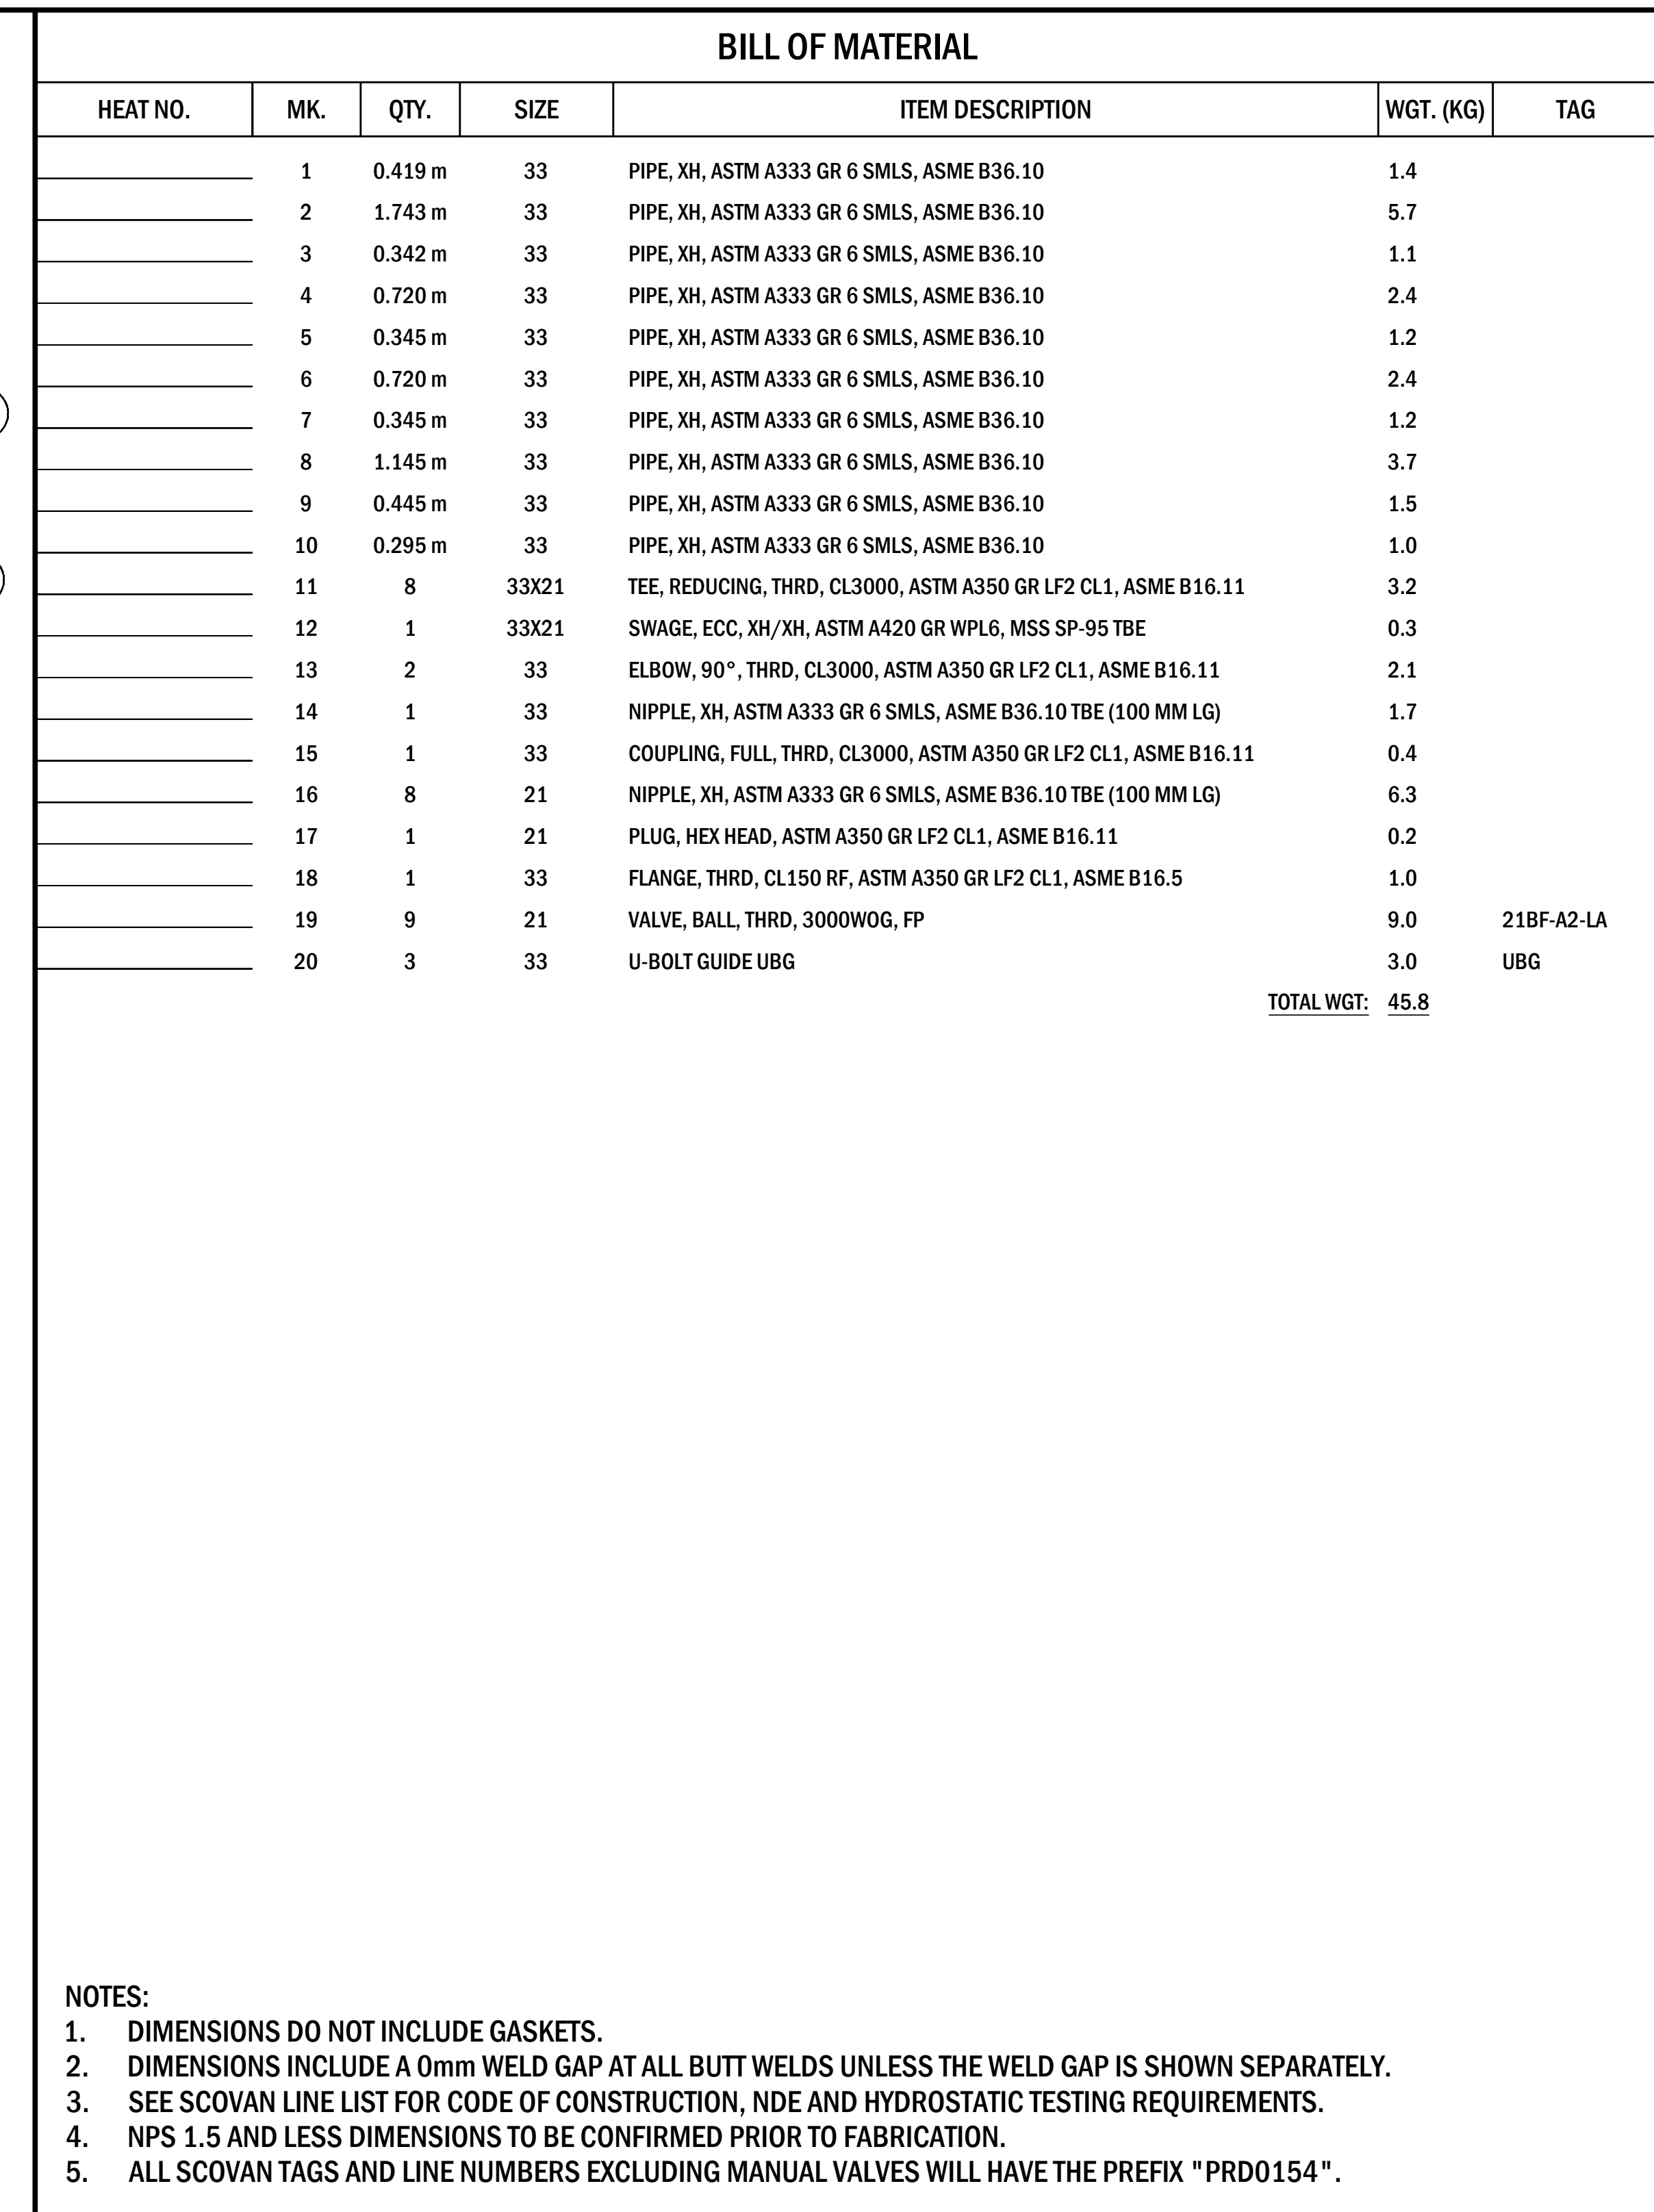

WELD MAP - SHOP USE ONLY																									CN. 018			MOD. NO.		WPS. -	
MK.	TYPE	WELDER	WPS	DATE	MK.	TYPE	WELDER	WPS	DATE	MK.	TYPE	WELDER	WPS	DATE	MK.	TYPE	WELDER	WPS	DATE	MK.	TYPE	WELDER	WPS	DATE	INSULATION -			PAINT -			
																									LINE NO. 33-IA-A2B1-P0108						
																									CLIENT DRAWING NO. -						
						SCOVAN INC. 2026.05.26 ISSUED FOR CONSTRUCTION																				PadX PARTNERSHIP Scovan	PADX NEXT GENERATION ENERGY SOLUTIONS PRODUCTION MODULE (MOD-01-P01) PIPING ISOMETRIC DRAWING CLIENT DRAWING NO. - DRAWING NO. G02-1-PRD0154-M-MSP-01-P01-P0108-01 REV. 1				
														1	ISSUED FOR CONSTRUCTION WITH OPTION(S) 3, 9					2026.1111	2026.05.26	AUTO	AUTO	AUTO							
														0	ISSUED FOR CONSTRUCTION					2026.1111	2026.05.26	AUTO	AUTO	AUTO							
DRAWING NO.	REFERENCE DRAWINGS				STAMPS APPLY TO CURRENT REVISION ONLY									REV.	DESCRIPTION					JOB No.	DATE	BY	CHK	PE							