




**ELEVATION VIEW**  
SCALE 1:20  
(LOOKING NORTH)

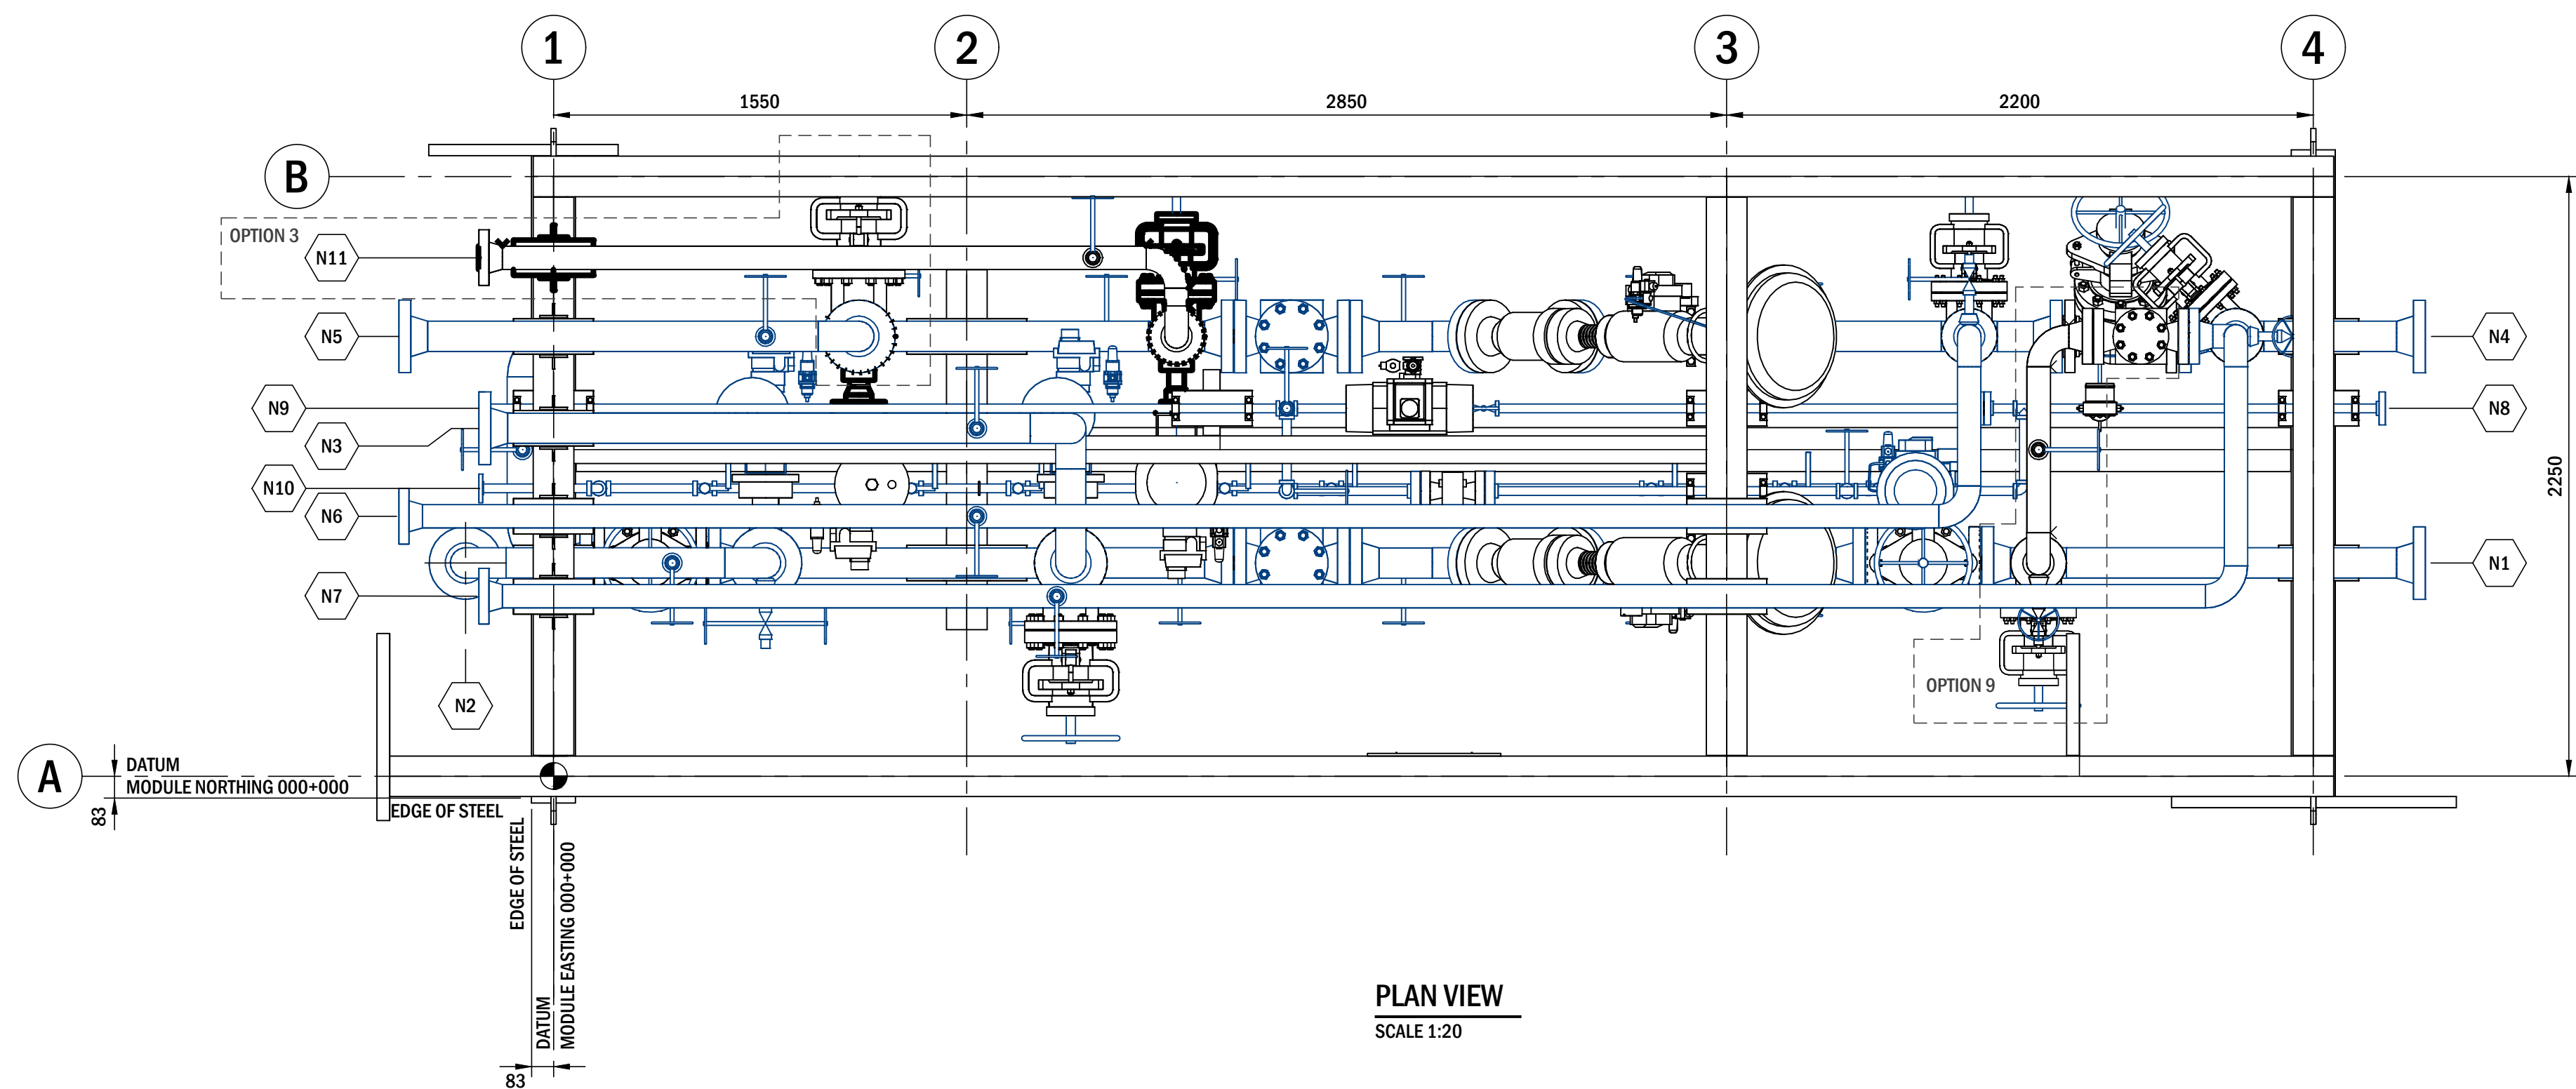

**NOTES:**

1. STAMPS APPLIED TO PIPING ONLY.
2. DATUM IS CENTRE LINE OF INTERSECTING BEAMS OF THE SW CORNER, RELATIVE TO MODULE NORTH AND TOP OF FLOOR PLATE WHEN CHECKERED PLATE IS USED, OR TOP OF MODULE STEEL WHEN GRATING IS USED.
3. OVERALL APPROXIMATE SHIPPING LENGTH 7829mm, WIDTH 3554mm, HEIGHT 3787mm.
4. APPROXIMATE SHIPPING WEIGHT 6881kg.
5. MODULE DESIGNED FOR STRAIGHT LIFT WITH CROSBY 3/4" G2140 BOLT TYPE SHAKK.
6. THIS DRAWING REFERENCES THE ENGINEERING RECORD G02-1-PRDXXX-N-PIP-01-P01-01 REV 0 FOR ALL TECHNICAL INFORMATION. IN THE EVENT OF DISCREPANCY BETWEEN THIS DRAWING AND THE ENGINEERED DRAWING OR RECORD, THE ENGINEERED DRAWING OF RECORD WILL TAKE PRECEDENCE UNLESS THE CHANGE IS PROPERLY CLOUDED AS A REVISION TO THIS DRAWING AND STAMPED BY A PROFESSIONAL ENGINEER.

DWG Path: C:\USERS\FORGEDOCGEN\DESKTOP\DWG TO PDF DATA\2026-05-27 00-14-17 22C5807A-C83A-414D-B736-C8571159EB8 PLOTTED BY: FORGEDOCGEN Plot Date: May 27, 26 @ 12:15 AM THIS DOCUMENT'S USE IS CONDITIONED UPON THE USER'S AGREEMENT NOT TO USE, DISCLOSE OR OTHERWISE DISSEMINATE DOCUMENT, IN WHOLE OR IN PART, FOR ANY PURPOSE EXCEPT AS SPECIFICALLY INTENDED BY SCOVA INC. ANY PRINTED VERSION OF THIS DOCUMENT IS A COPY AND IS NOT A REPRESENTATION OF THE ORIGINALLY AUTHENTICATED DOCUMENT.