



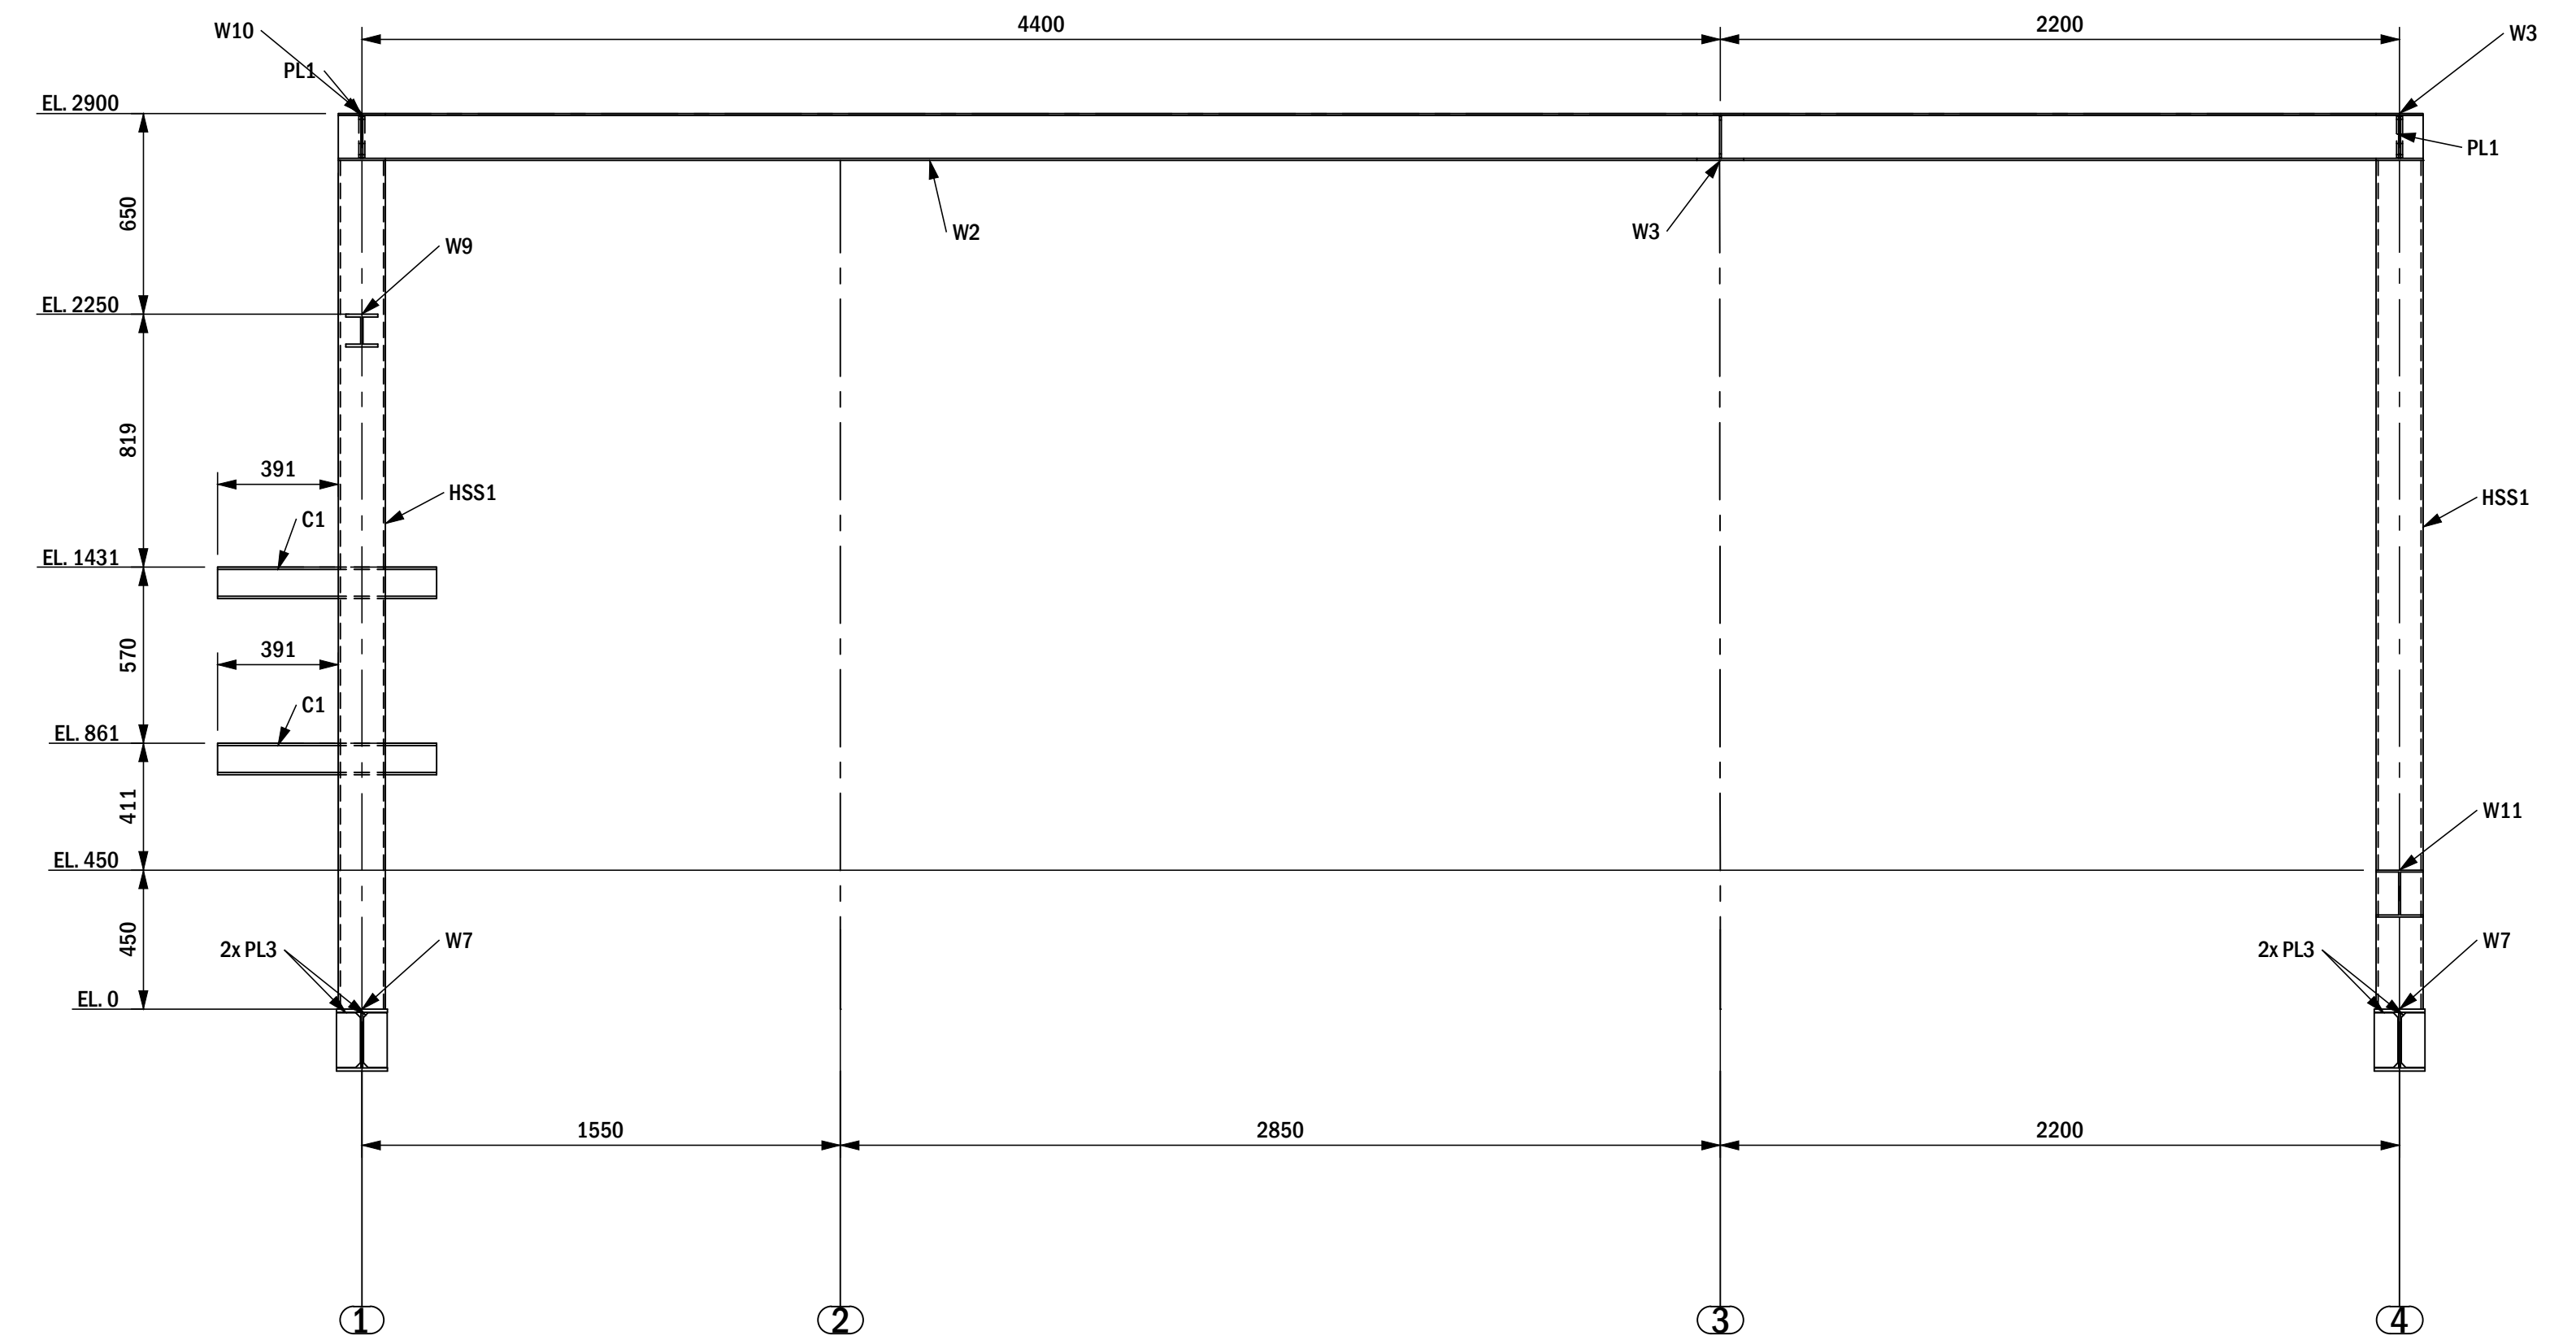

ELEVATION AT GRID LINE "A"
SCALE 1:20

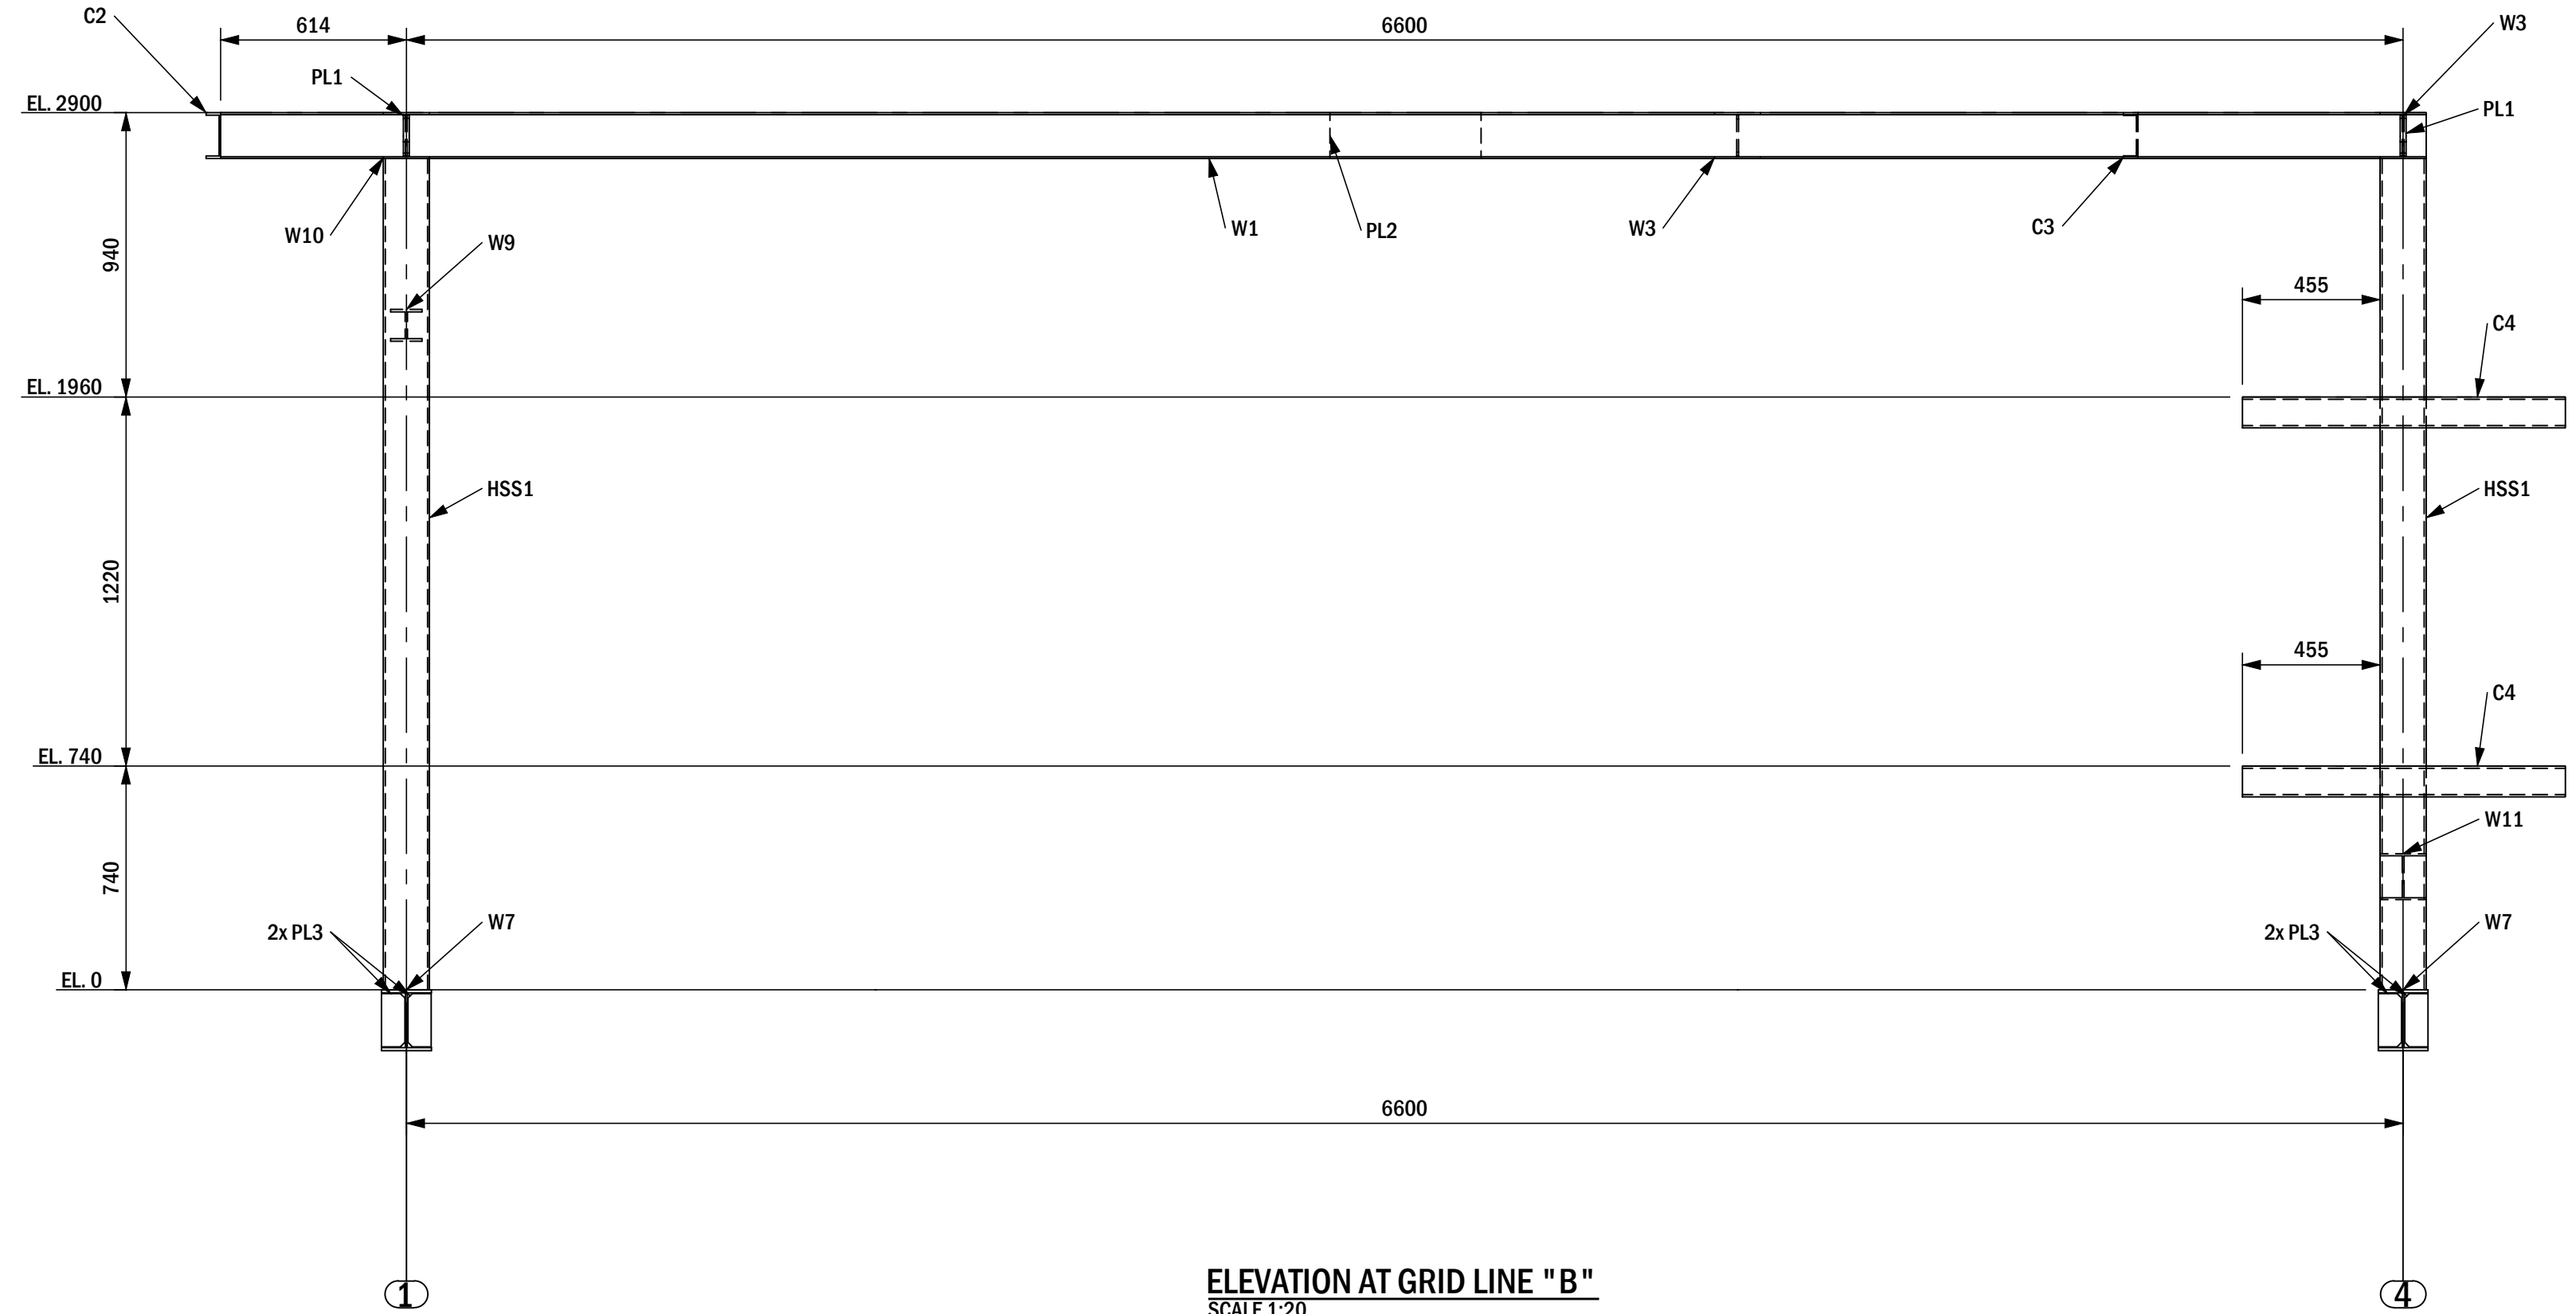

ELEVATION AT GRID LINE "B"
SCALE 1:20

REFER TO STANDARD
STRUCTURAL NOTES
0110100-S-NOTE-00-001-01

GENERAL NOTES:
1. THIS DRAWING REFERENCES THE ENGINEERING RECORD G02-1-PRD0154-S-STR-01-P01-04 REV 0 FOR ALL TECHNICAL INFORMATION. IN THE EVENT OF DISCREPANCY BETWEEN THIS DRAWING AND THE ENGINEERED DRAWING OF RECORD, THE ENGINEERED DRAWING OF RECORD WILL TAKE PRECEDENCE UNLESS THE CHANGE IS PROPERLY CLOUDED AS A REVISION TO THIS DRAWING AND STAMPED BY A PROFESSIONAL ENGINEER.

WPS. SCO-FCAW-CS R.1
SCO-SMAW-CS R.1

--	--	