




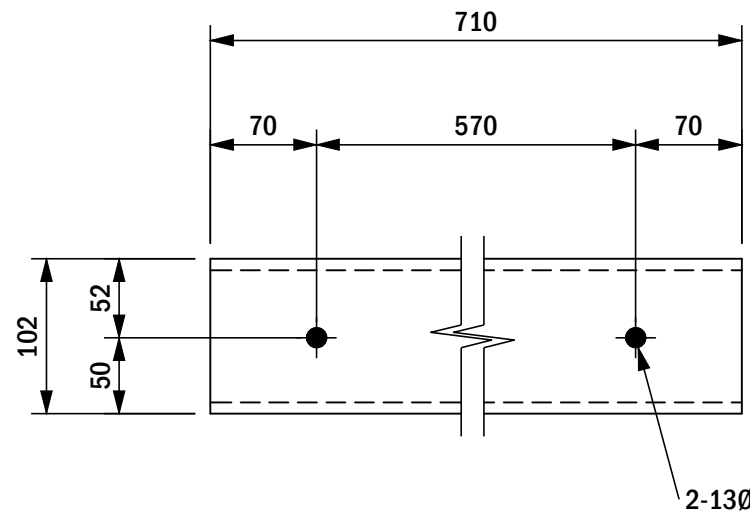


C1
SCALE 1:5
2 REQUIRED

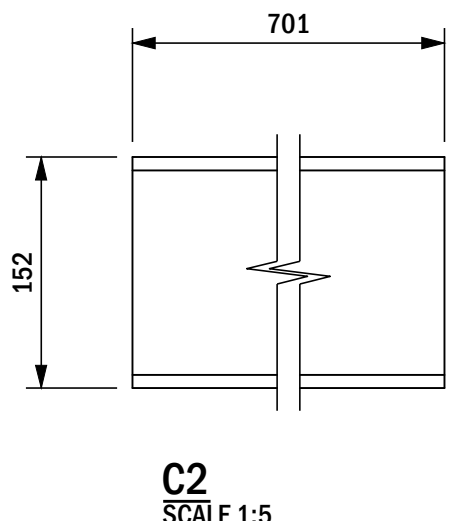


C2
SCALE 1:5
1 REQUIRED

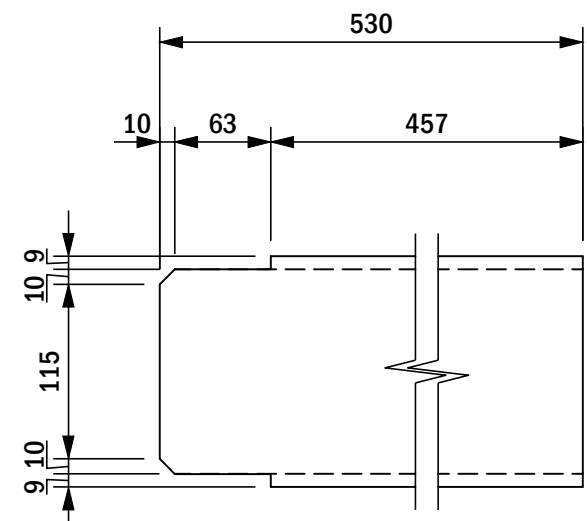


C3
SCALE 1:5
1 REQUIRED

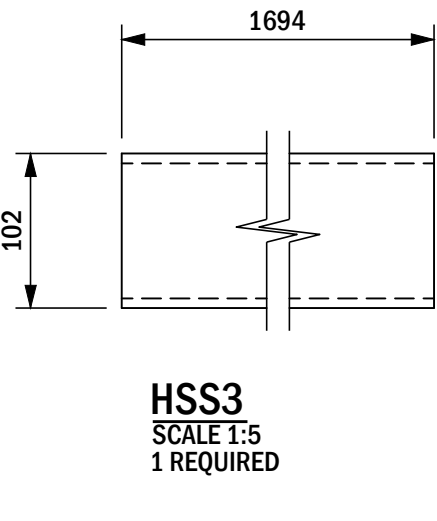


HSS3
SCALE 1:5
1 REQUIRED

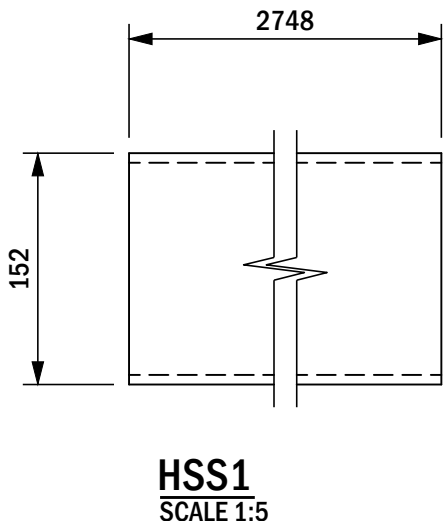


HSS1
SCALE 1:5
5 REQUIRED

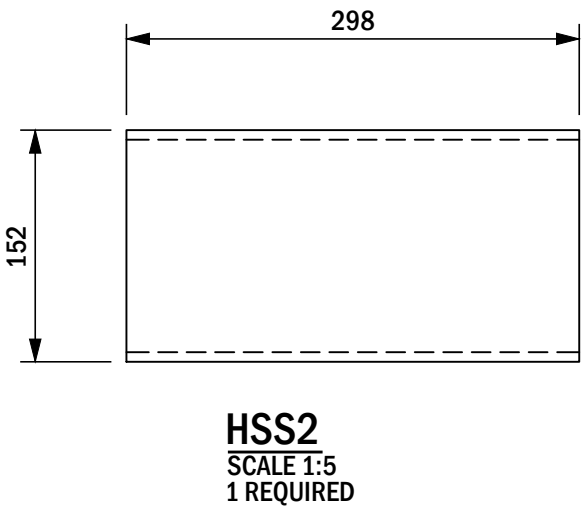


HSS2
SCALE 1:5
1 REQUIRED

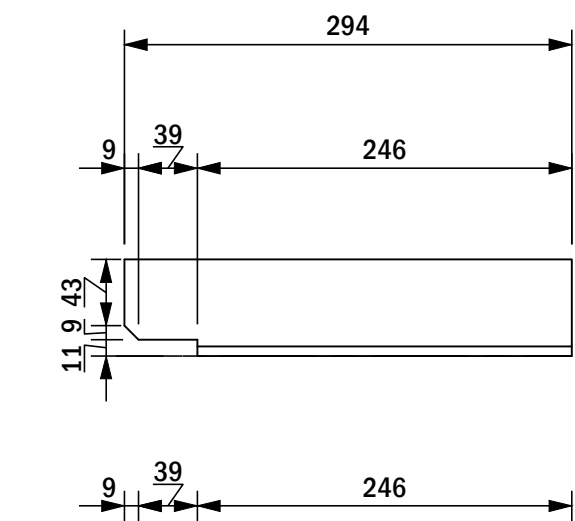


L2
SCALE 1:5
1 REQUIRED

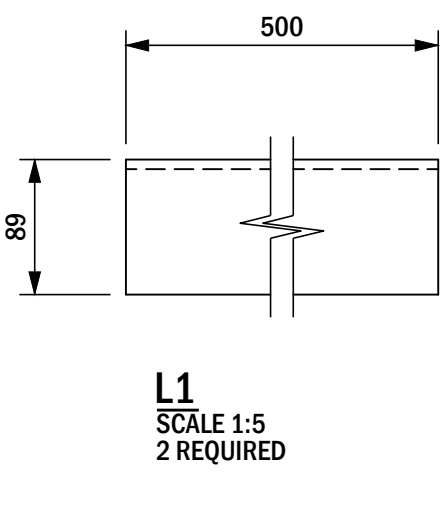


L1
SCALE 1:5
2 REQUIRED

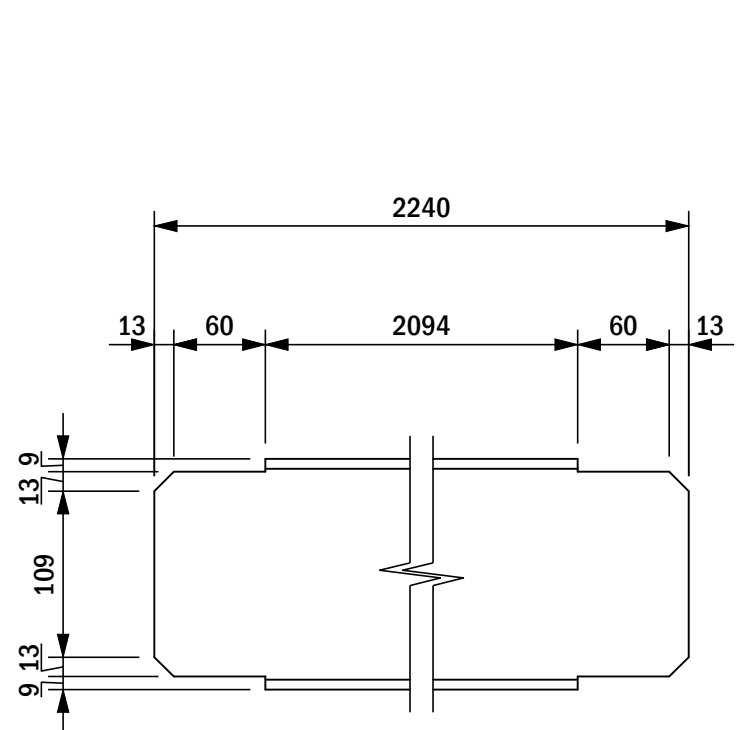


W3
SCALE 1:5
2 REQUIRED

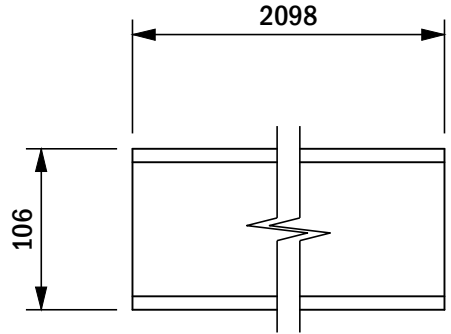


W9
SCALE 1:5
1 REQUIRED

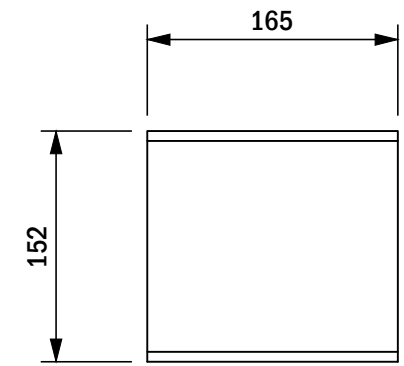


W5
SCALE 1:5
2 REQUIRED

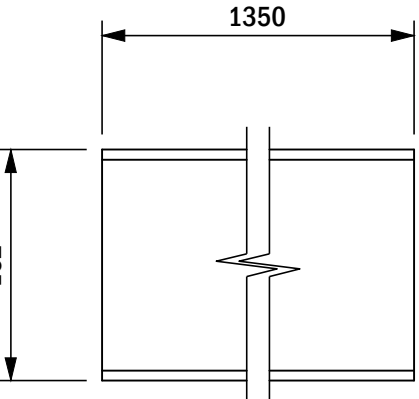


W12
SCALE 1:5
1 REQUIRED

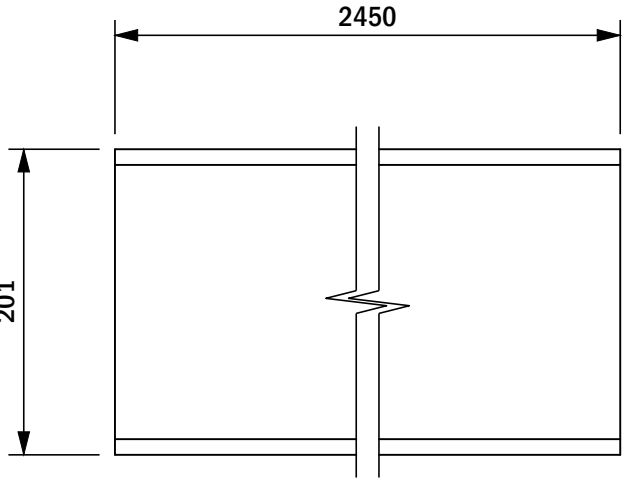


W7
SCALE 1:5
2 REQUIRED

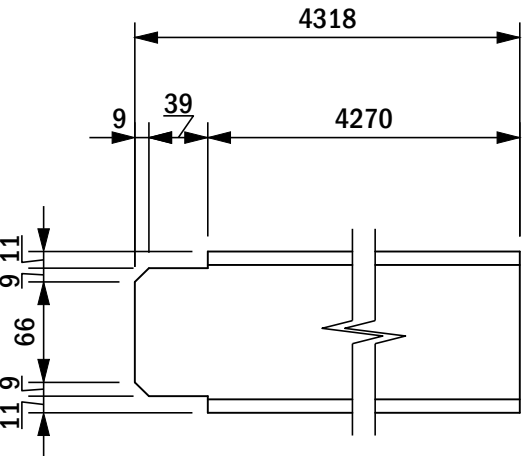


W8
SCALE 1:5
1 REQUIRED

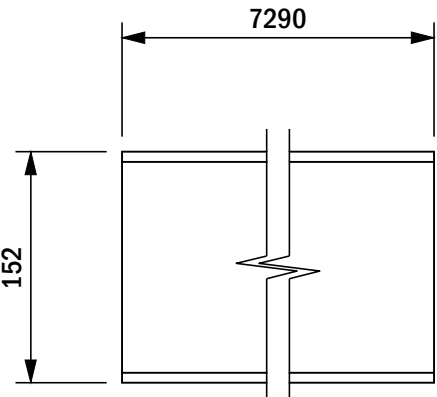


W1
SCALE 1:5
1 REQUIRED

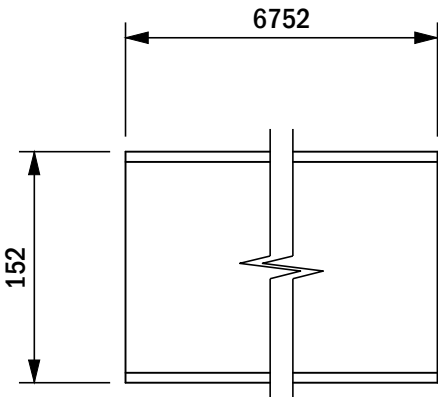


W2
SCALE 1:5
1 REQUIRED

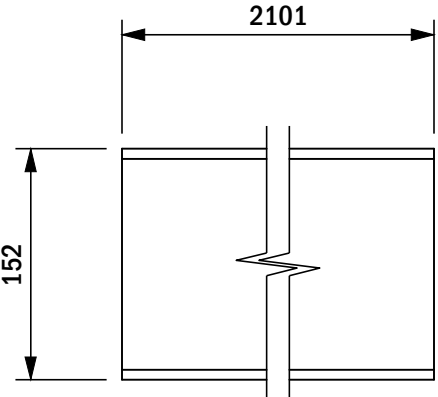


W11
SCALE 1:5
1 REQUIRED

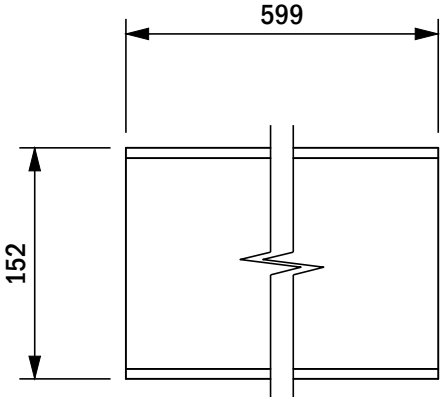


W4
SCALE 1:5
2 REQUIRED

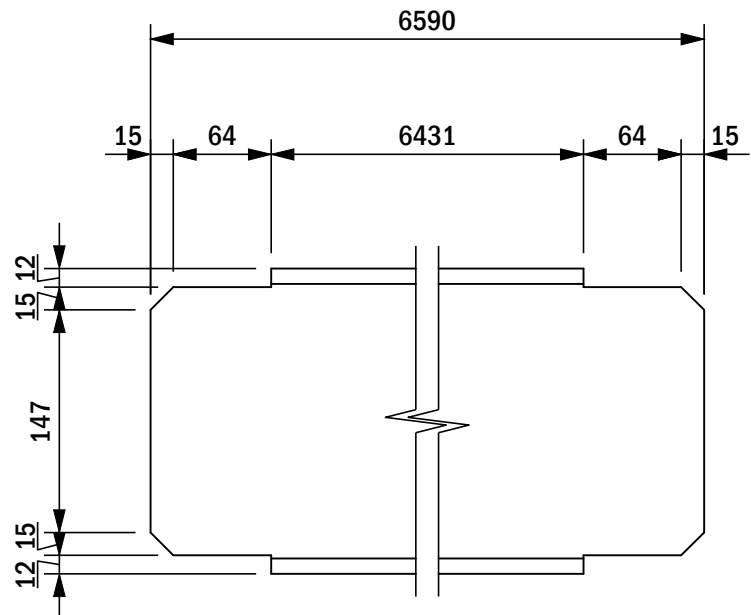


W6
SCALE 1:5
1 REQUIRED

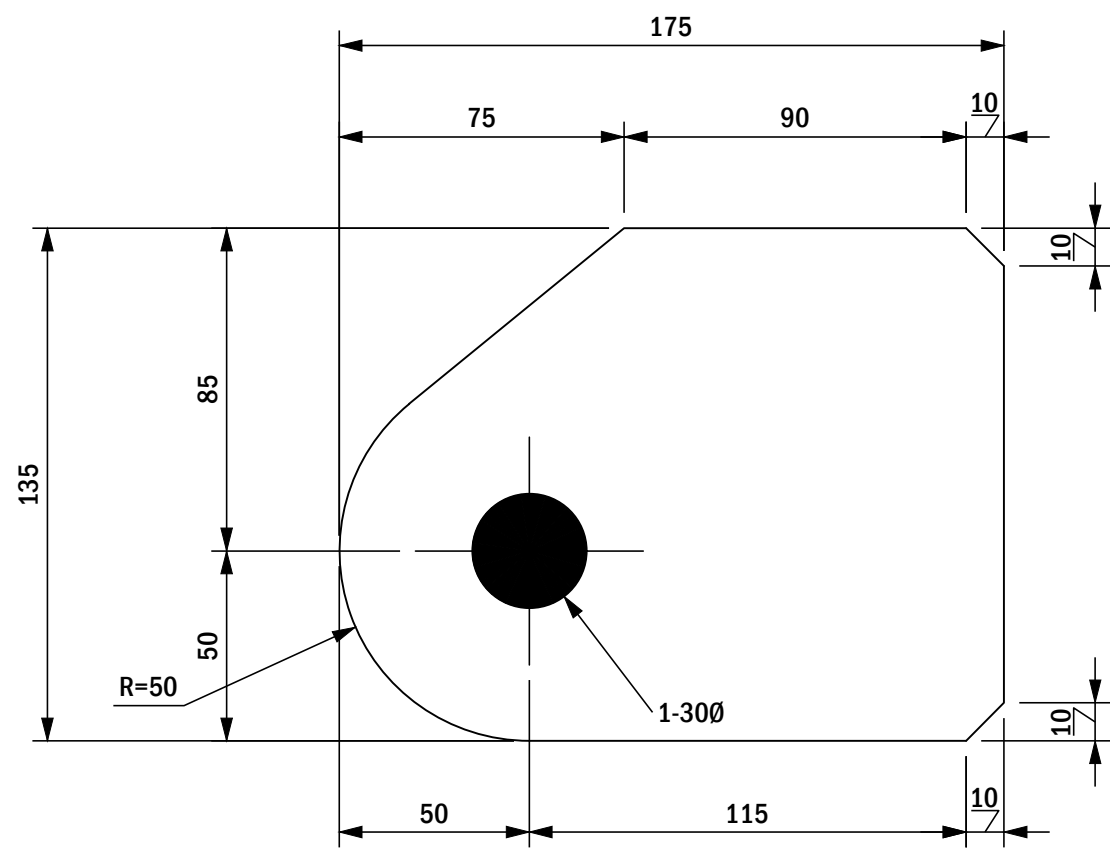


PL1
SCALE 1:2
4 REQUIRED

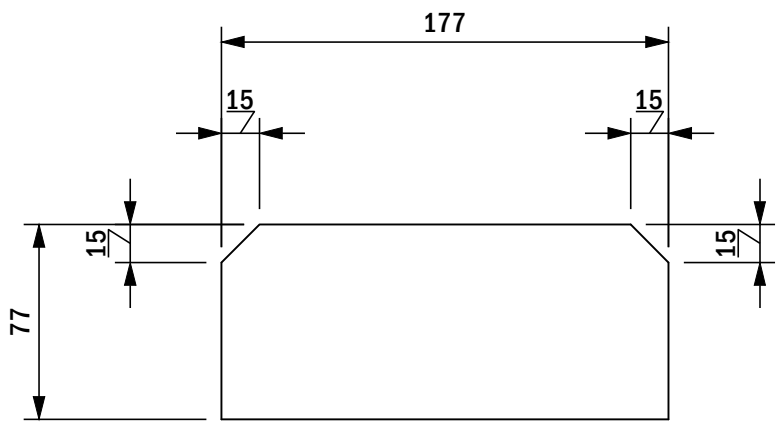

PL3
SCALE 1:3
10 REQUIRED

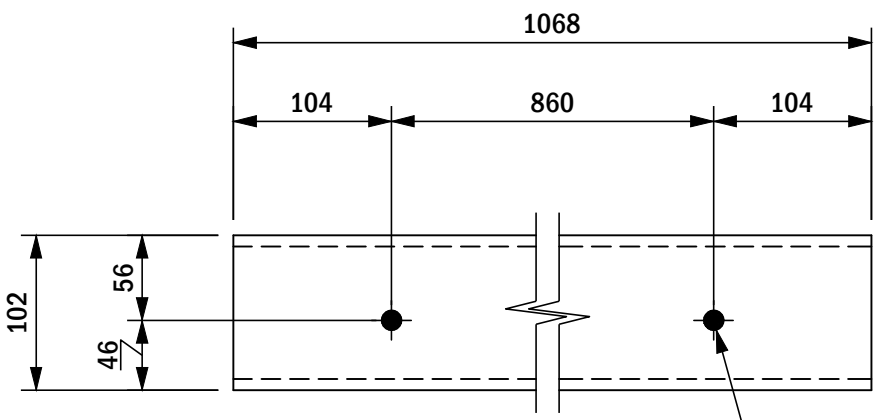

C4
SCALE 1:5
2 REQUIRED

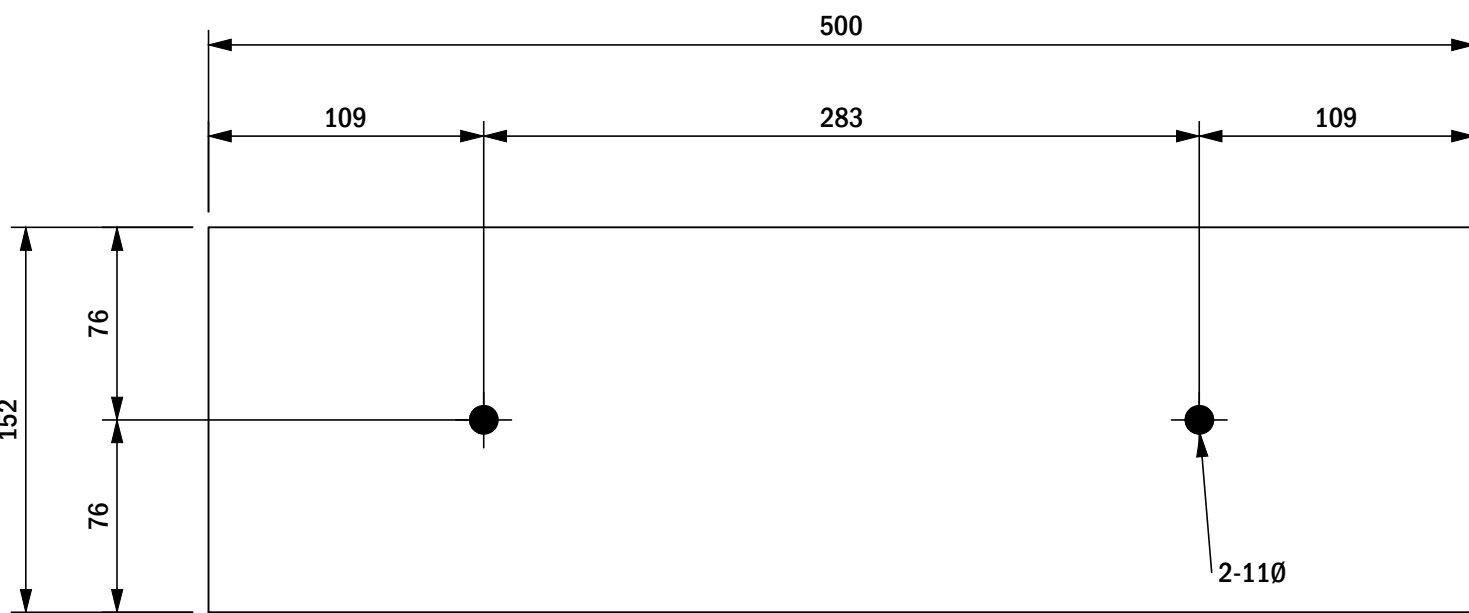

PL2
SCALE 1:3
1 REQUIRED

REFER TO STANDARD
STRUCTURAL NOTES
0110100-S-NOTE-00-001-01

GENERAL NOTES:
1. THIS DRAWING REFERENCES THE ENGINEERING RECORD G02-1-PRD0154-S-STR-01-P01-06 REV 0 FOR ALL TECHNICAL INFORMATION. IN THE EVENT OF DISCREPANCY BETWEEN THIS DRAWING AND THE ENGINEERED DRAWING OF RECORD, THE ENGINEERED DRAWING OF RECORD WILL TAKE PRECEDENCE UNLESS THE CHANGE IS PROPERLY CLOUDED AS A REVISION TO THIS DRAWING AND STAMPED BY A PROFESSIONAL ENGINEER.

WPS.
SCO-FCAW-CS R.1
SCO-SMAW-CS R.1

--	--	